

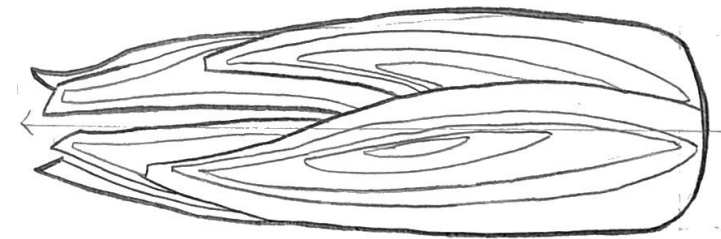
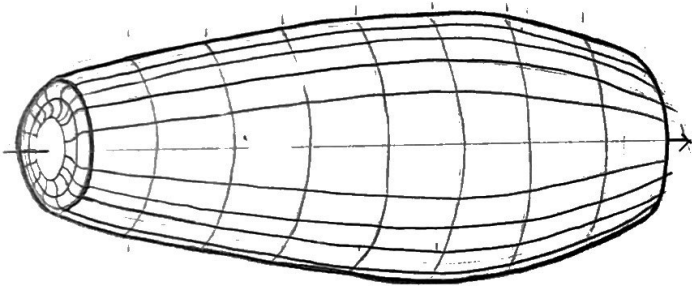
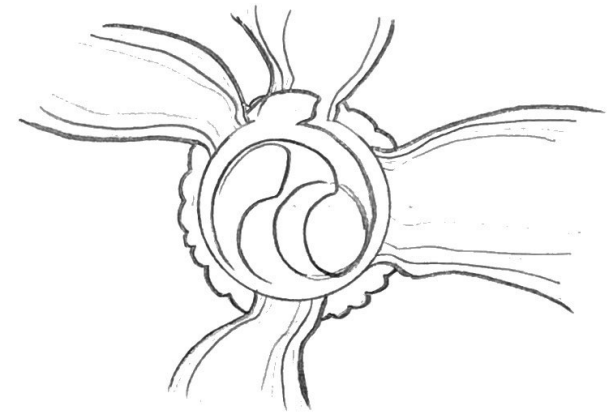
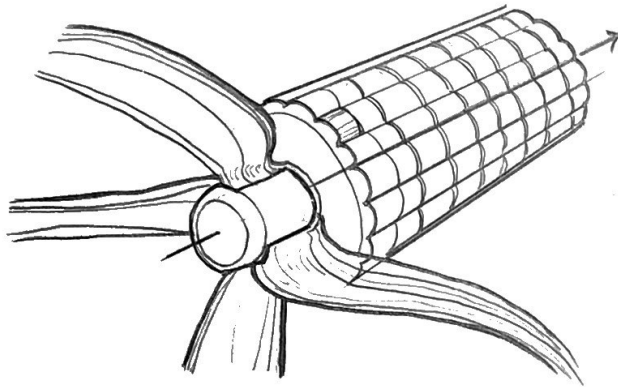
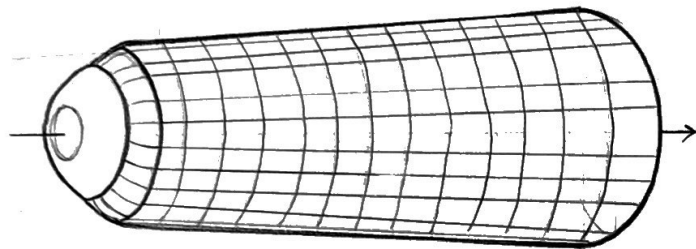
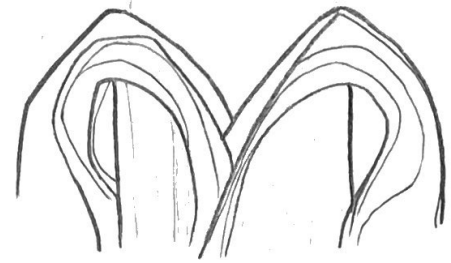
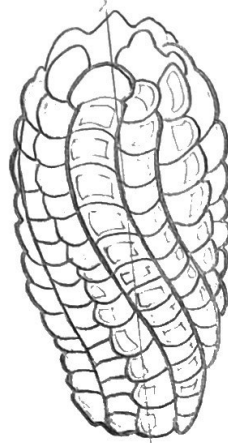
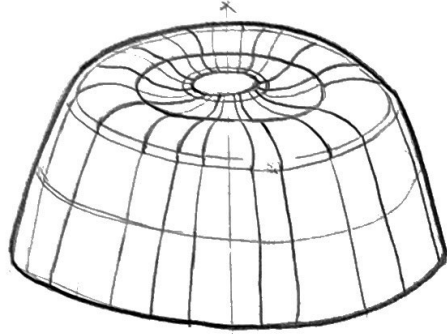
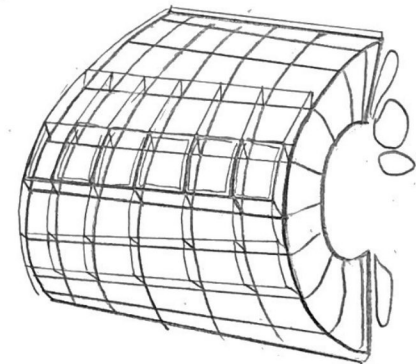
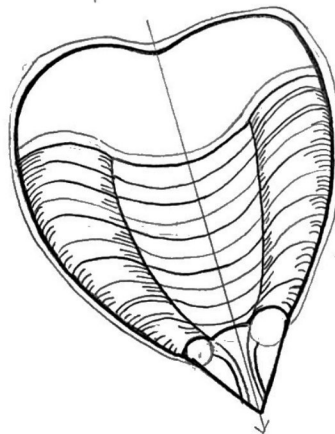
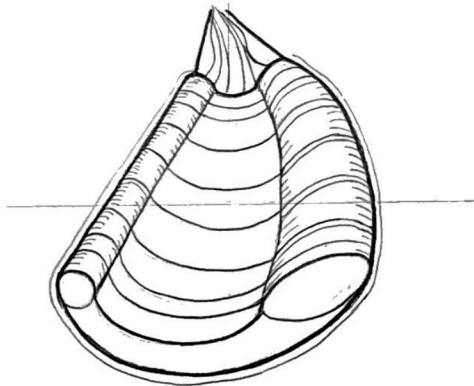
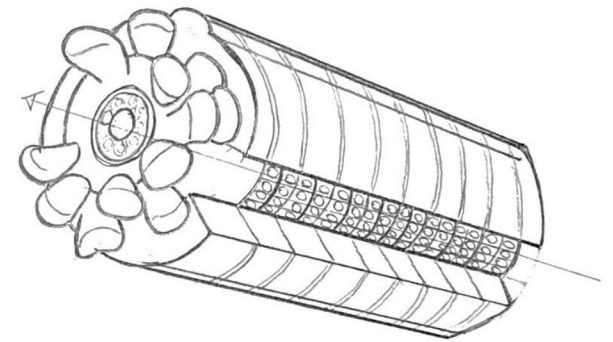
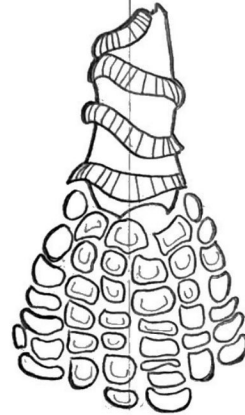
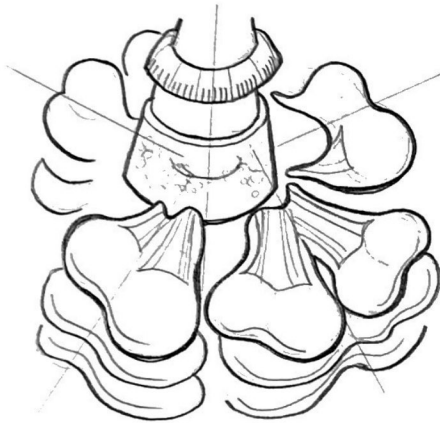
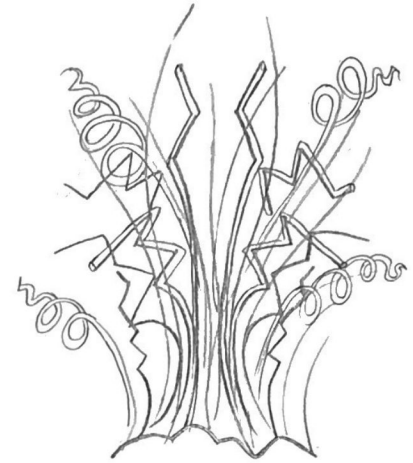










ZURIEL JUDE OLALIA


THE LIVING MARKET
ARCHITECTURAL DESIGN STUDIO
ARCHITECTURE-EGIS
HERIOT-WATT UNIVERSITY DUBAI
2025/26









"FLOWFIELD"









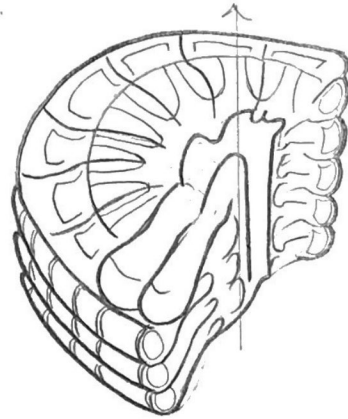


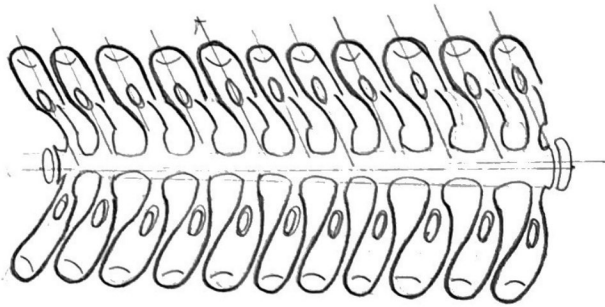


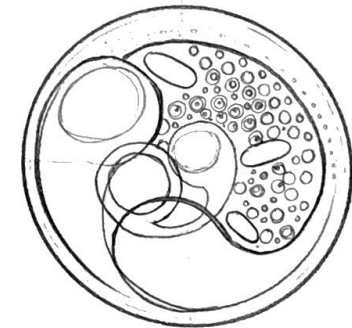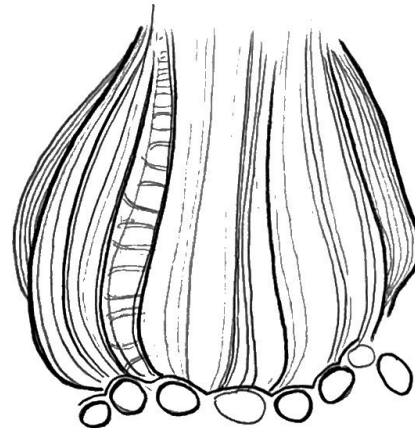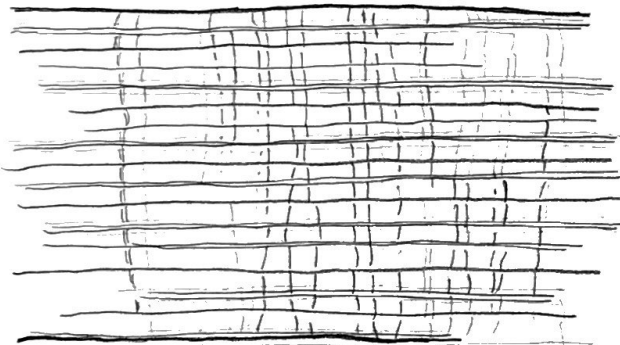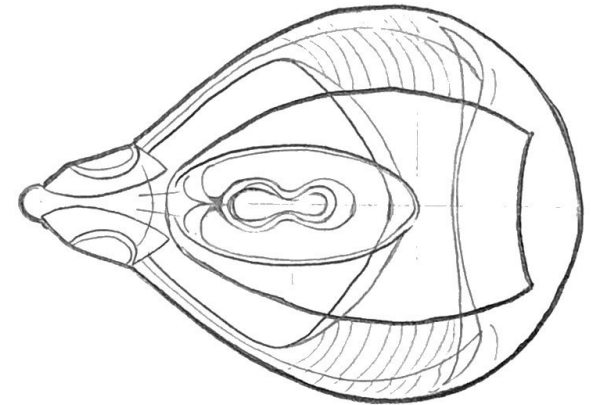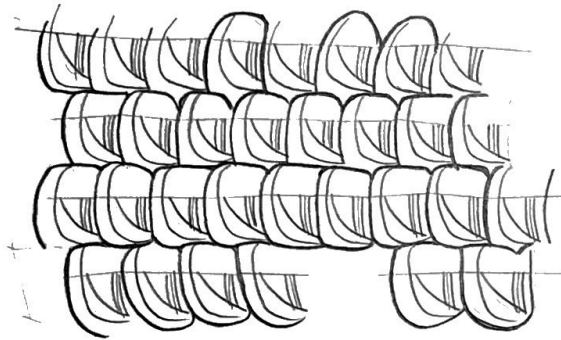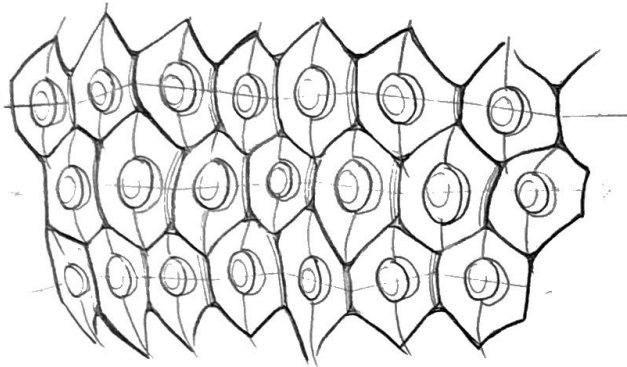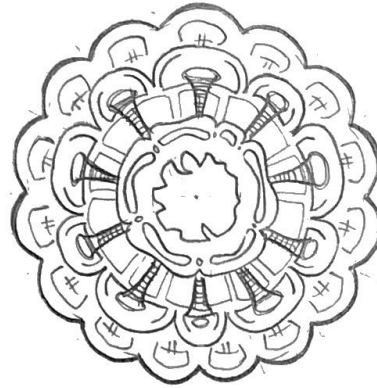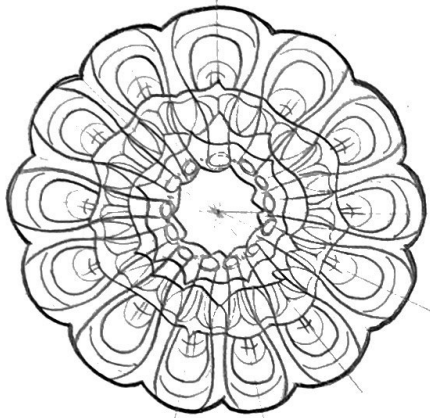

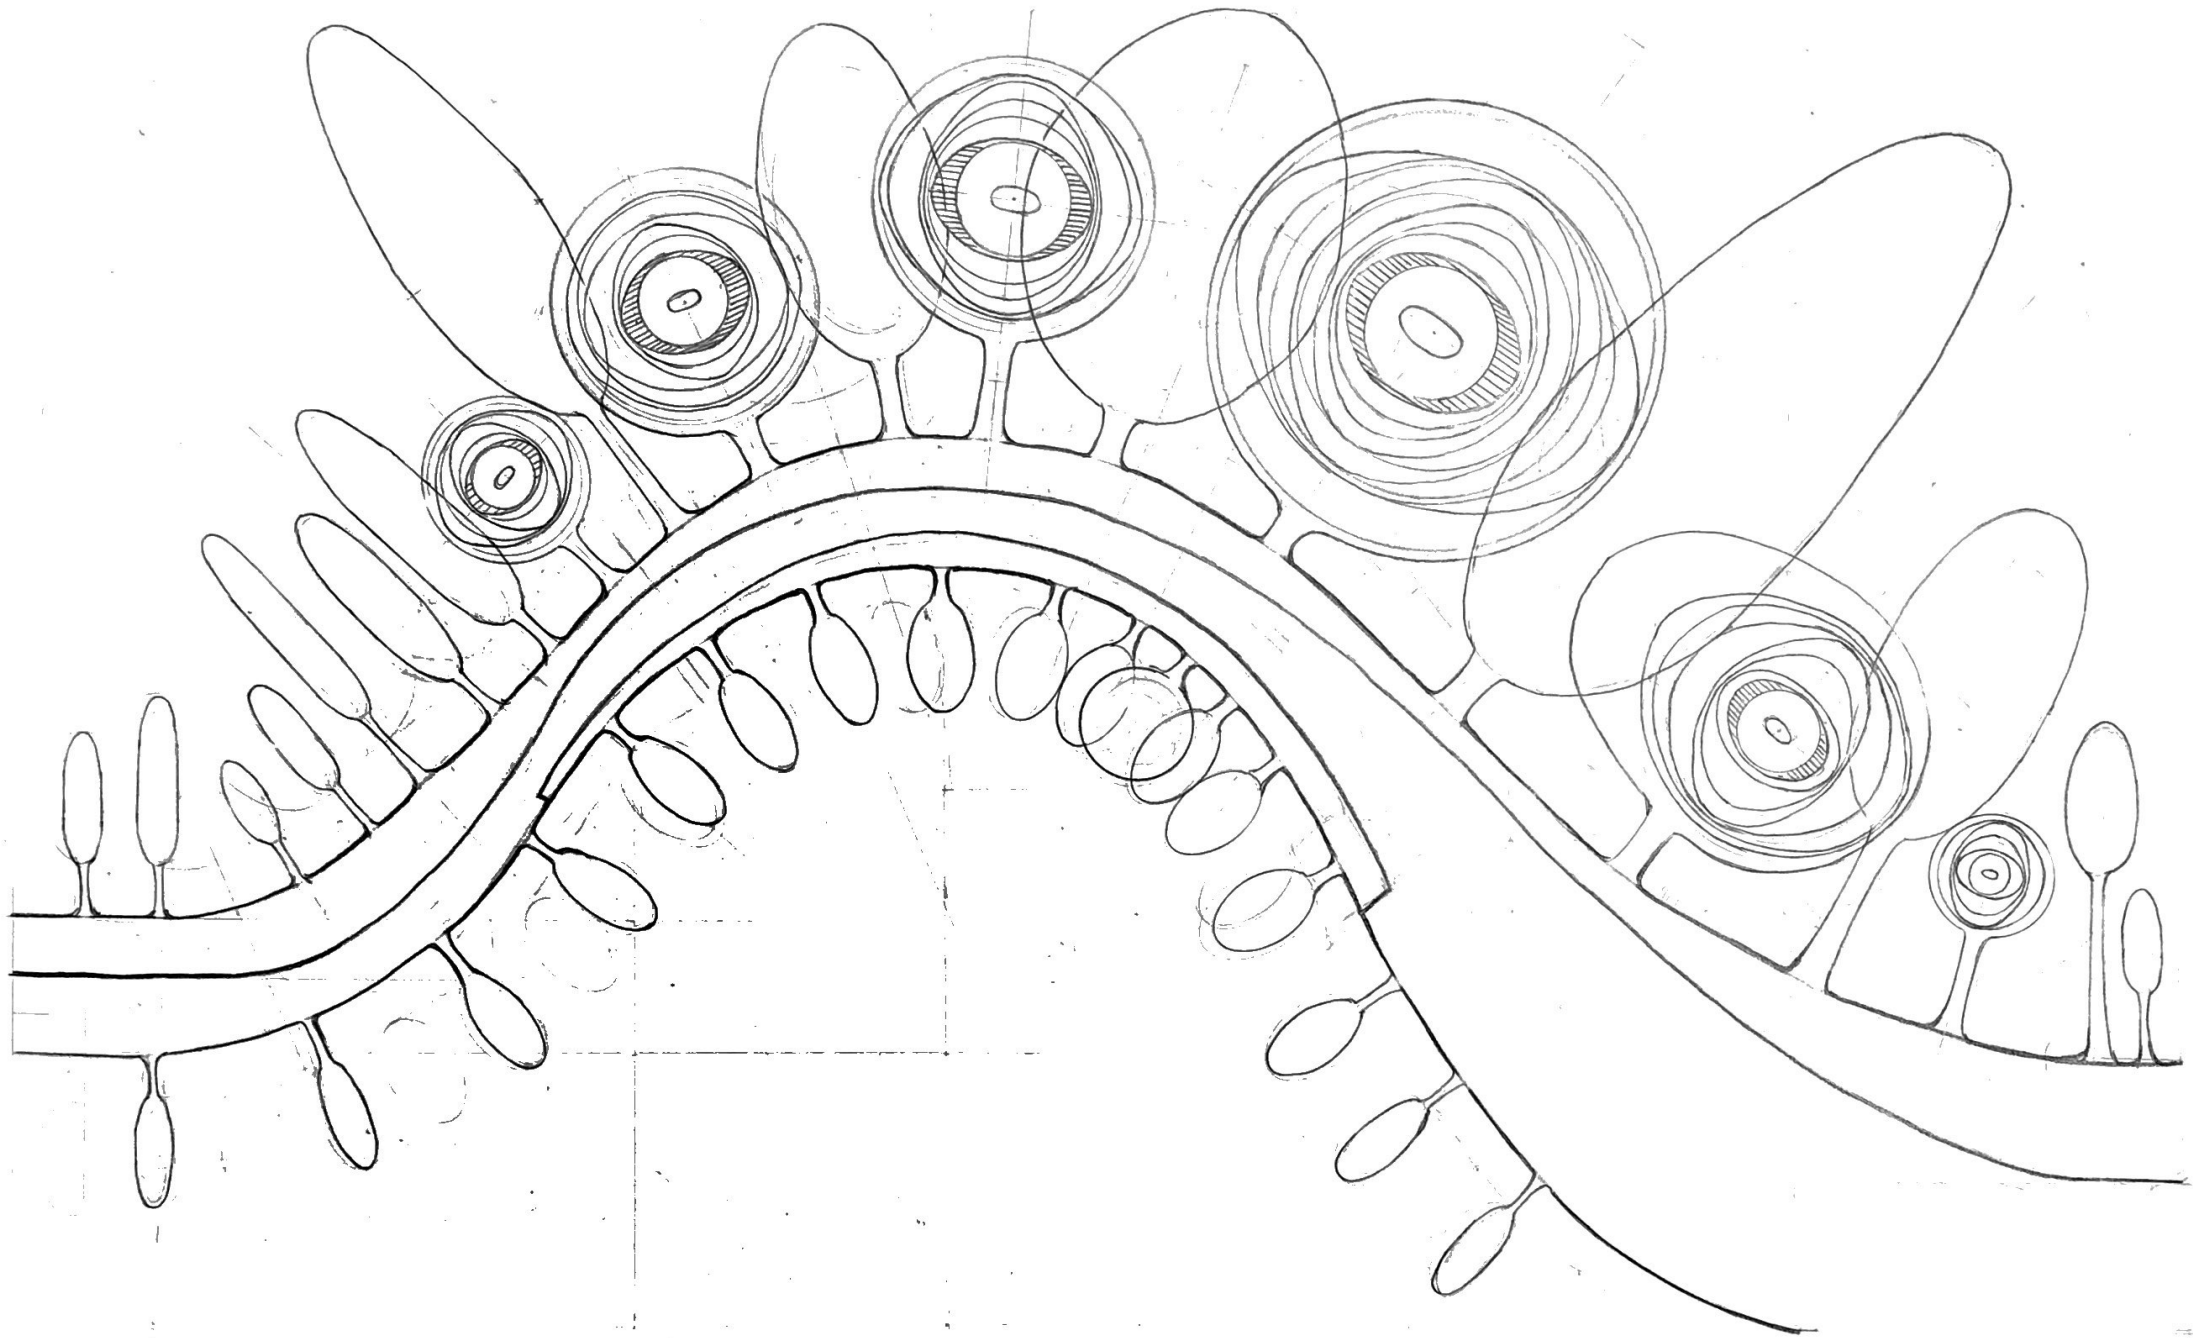

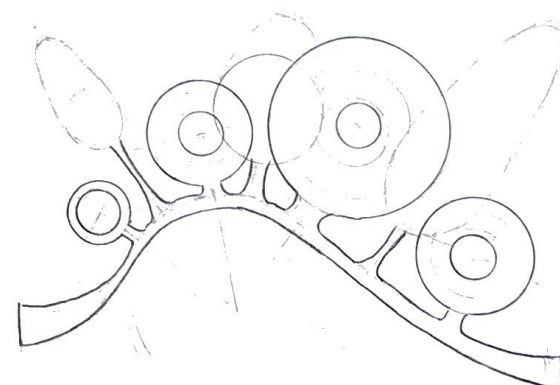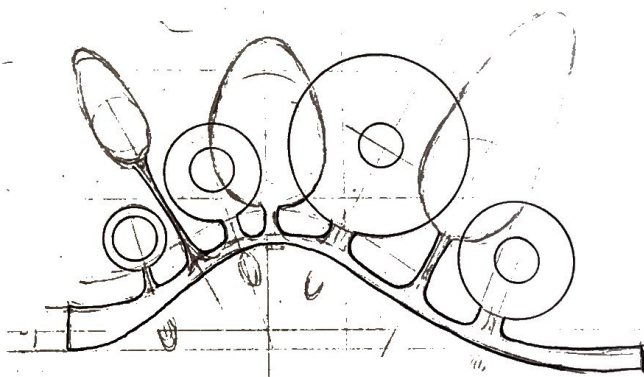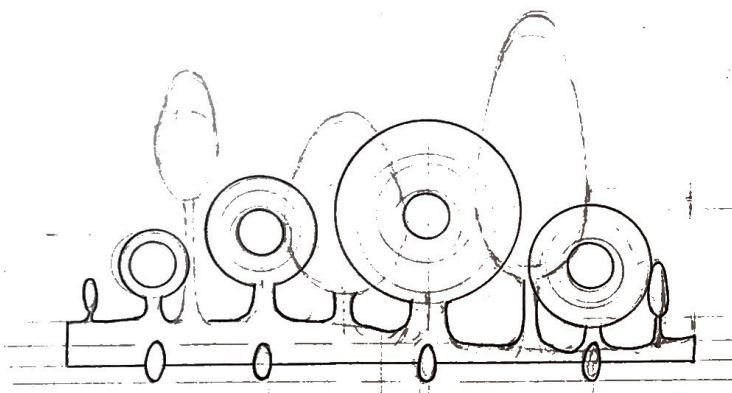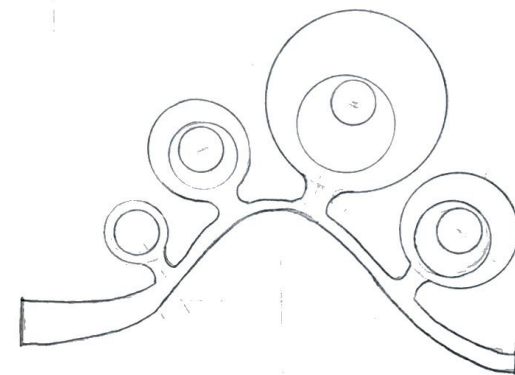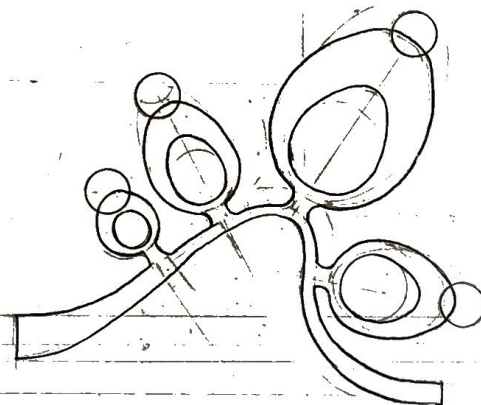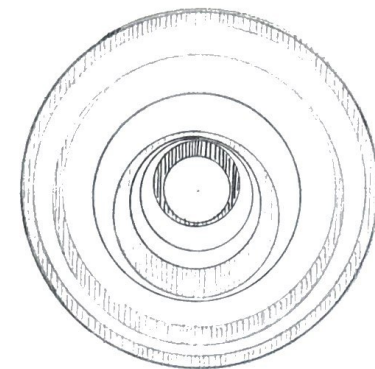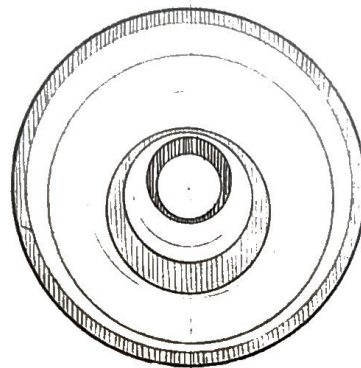
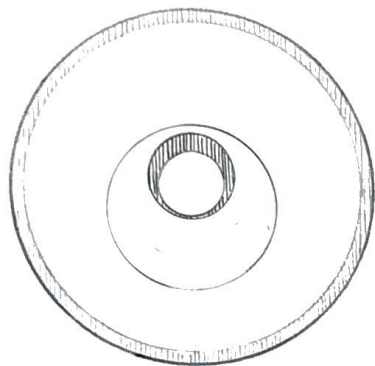


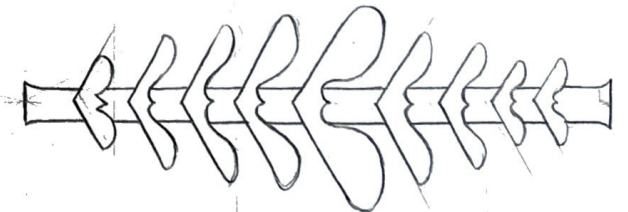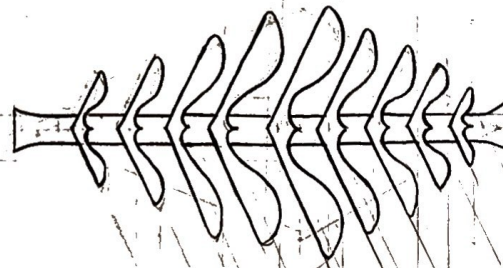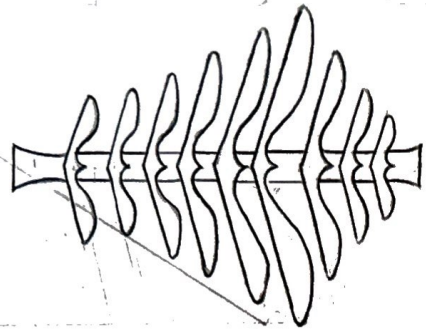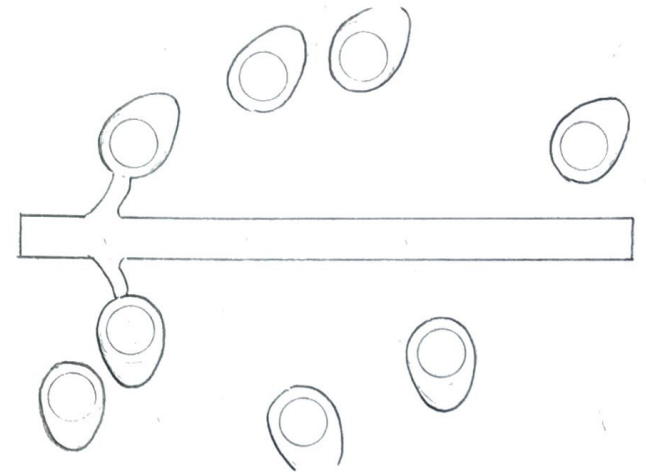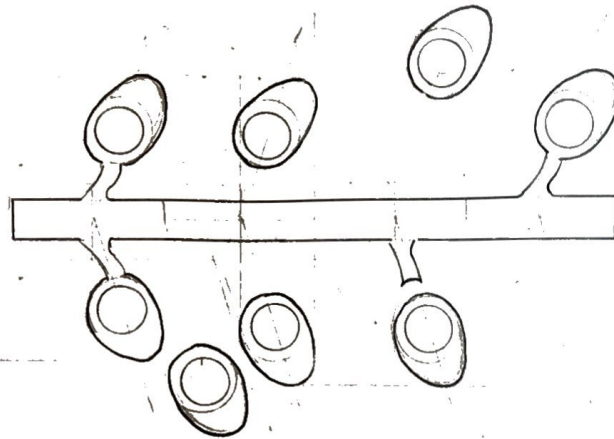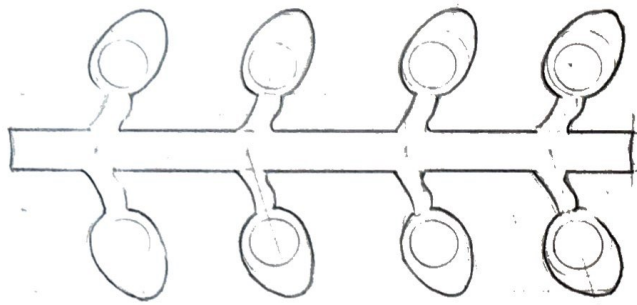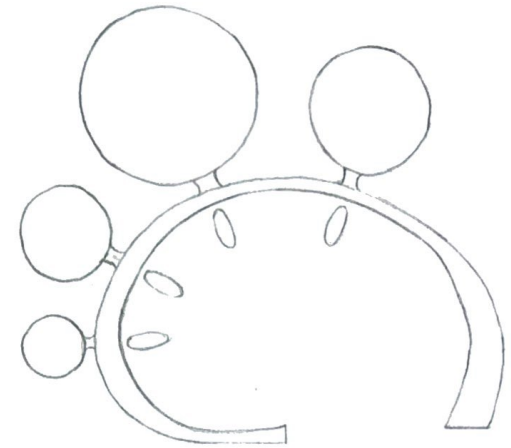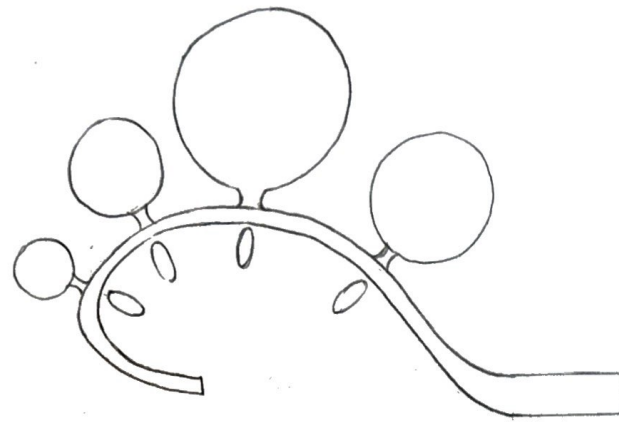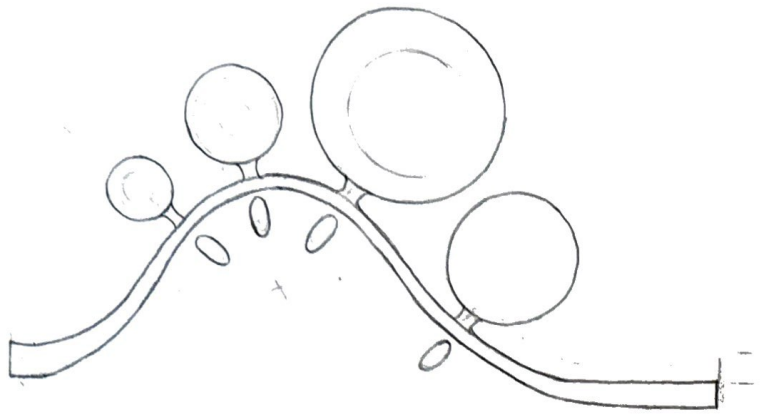

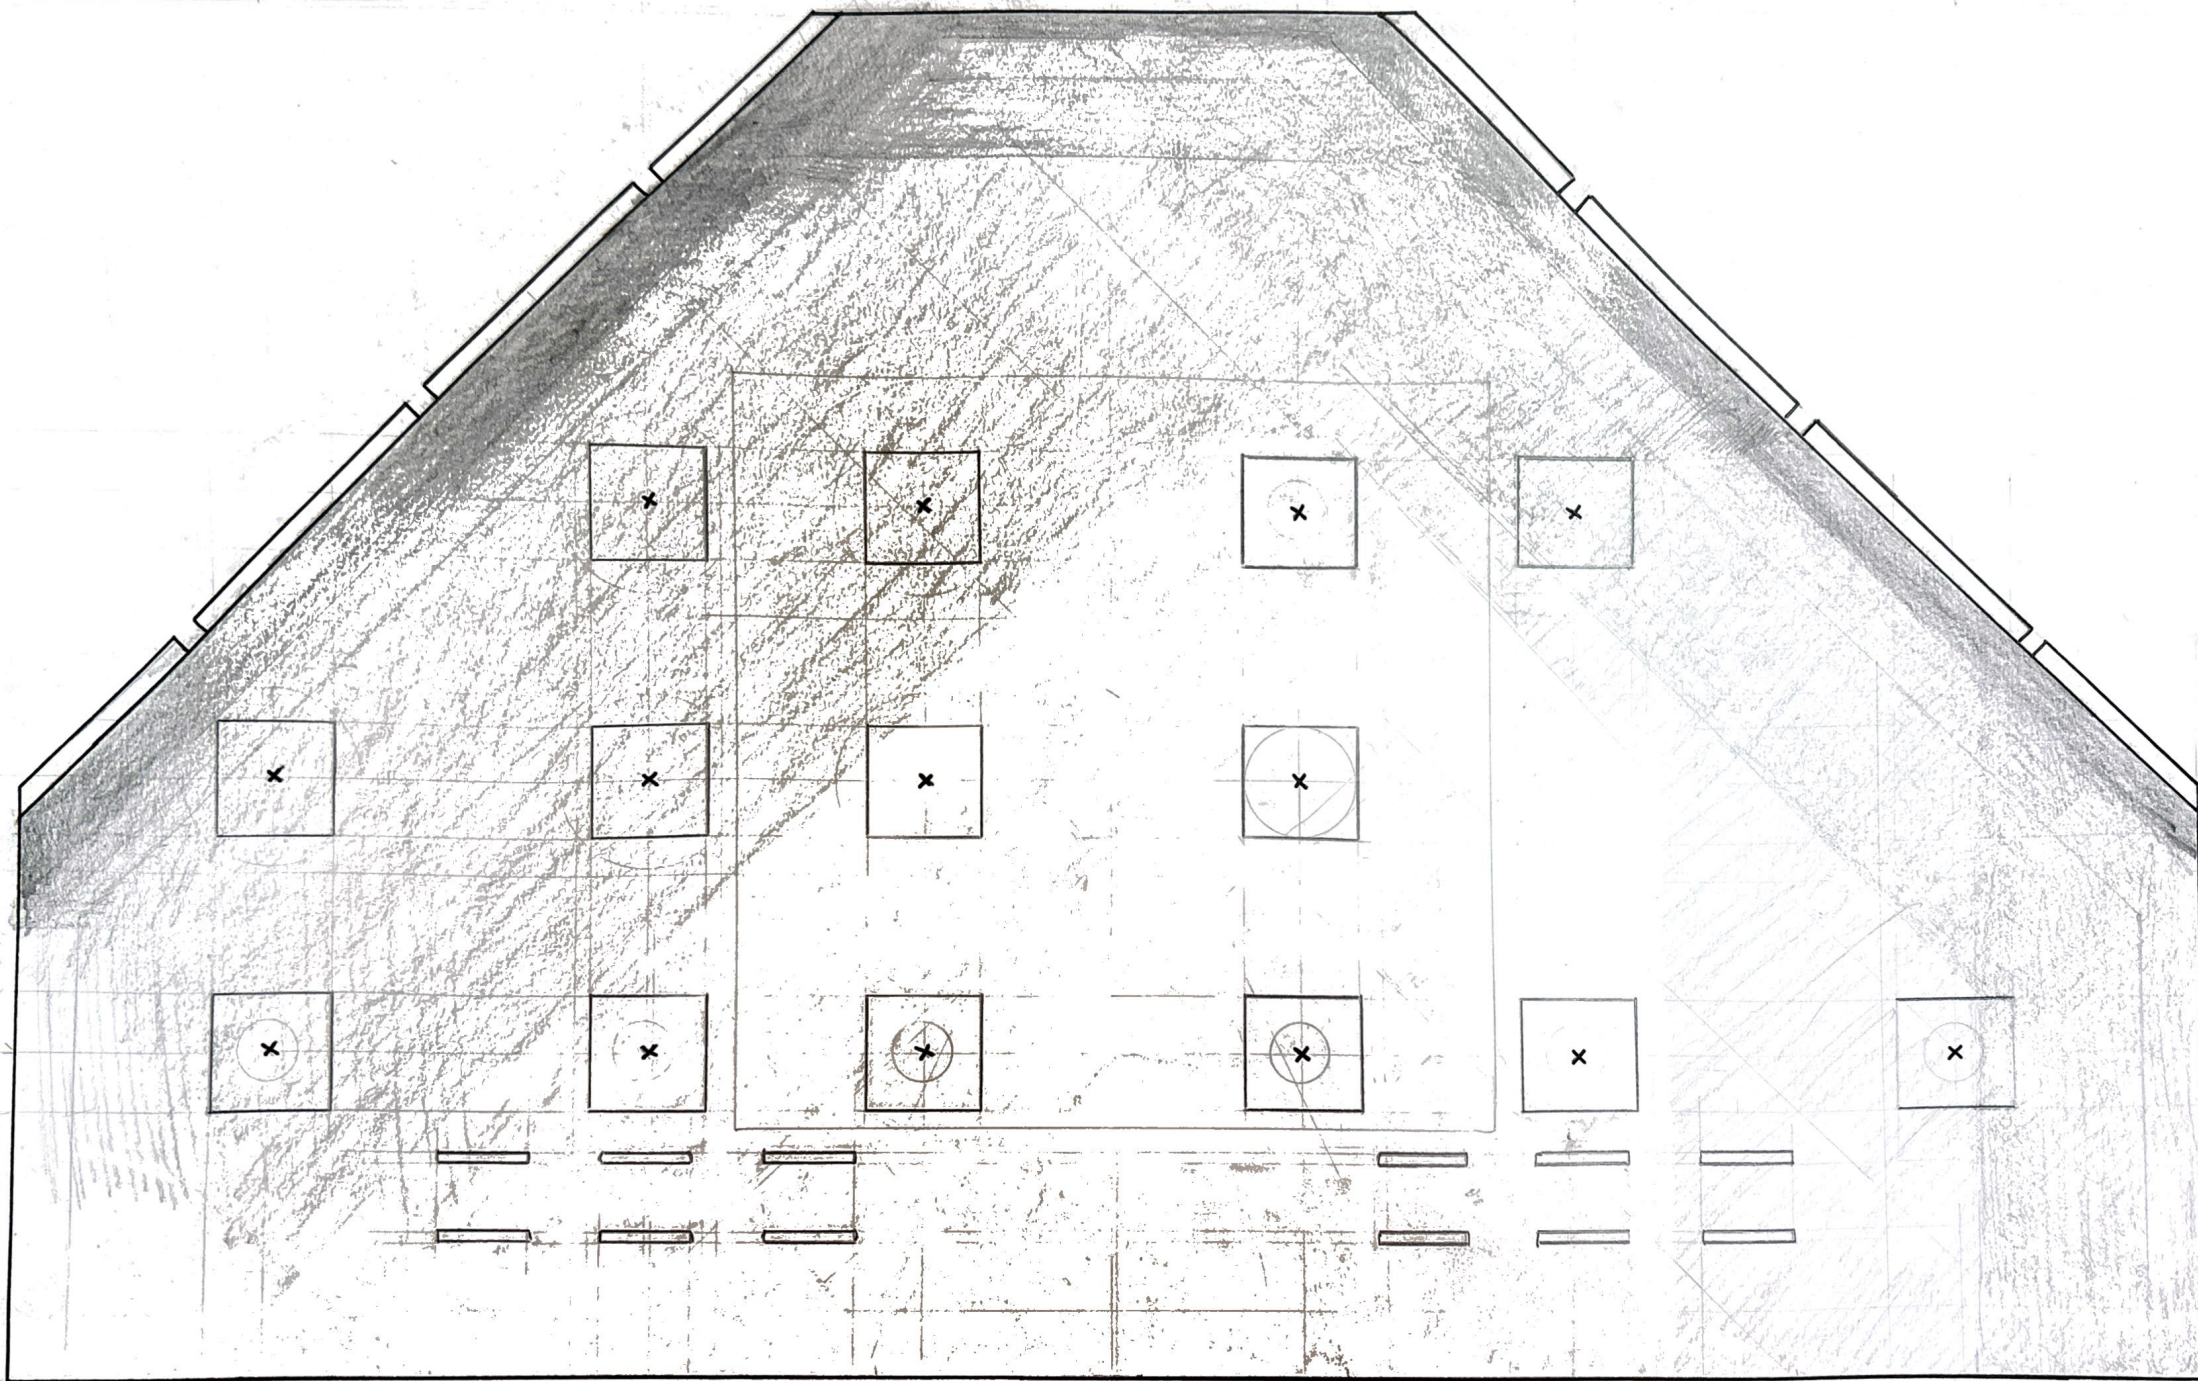



ACCESS AND CIRCULATION

SHADOWS (WINTER)

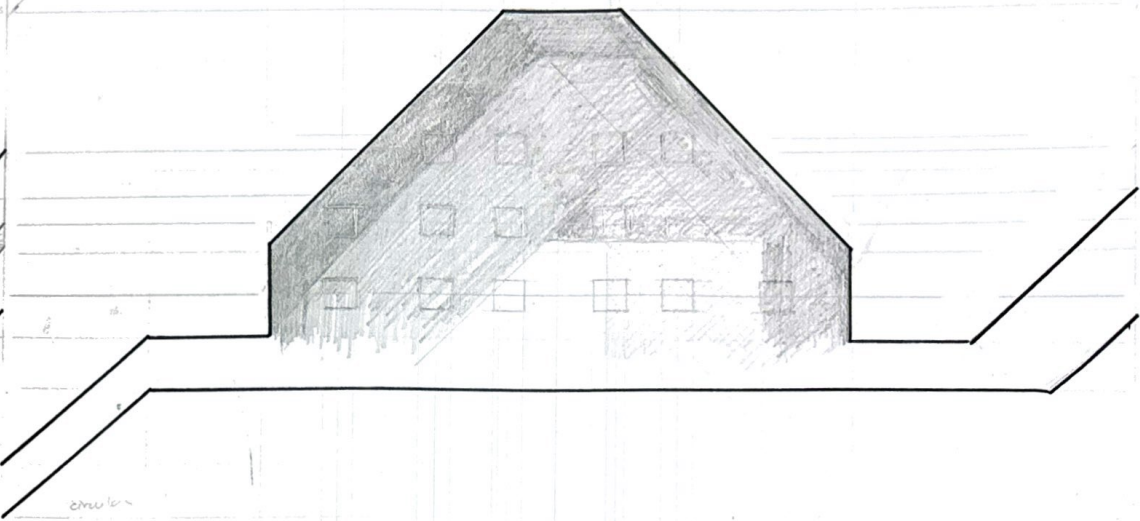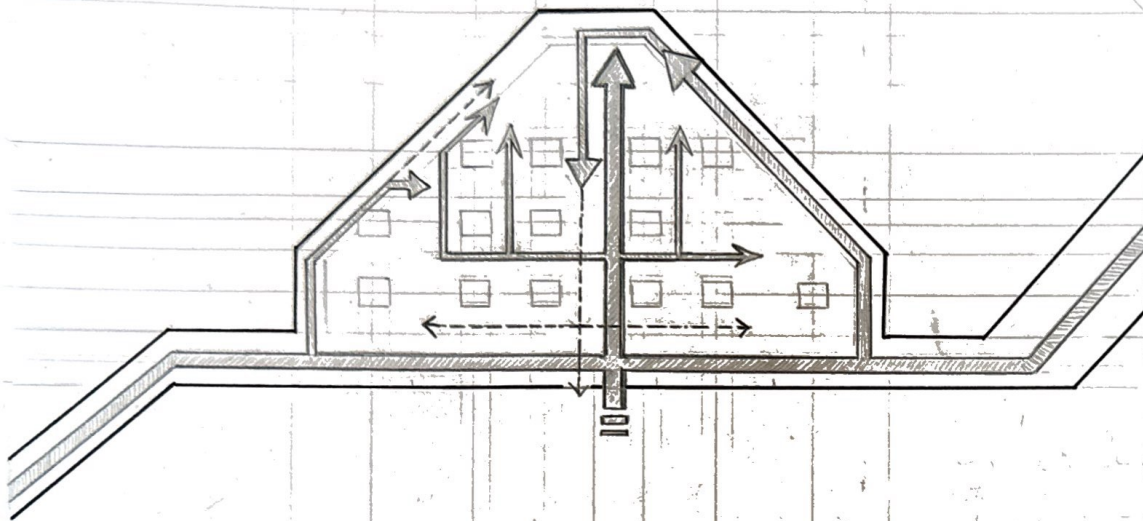


WIND

VEGETATION

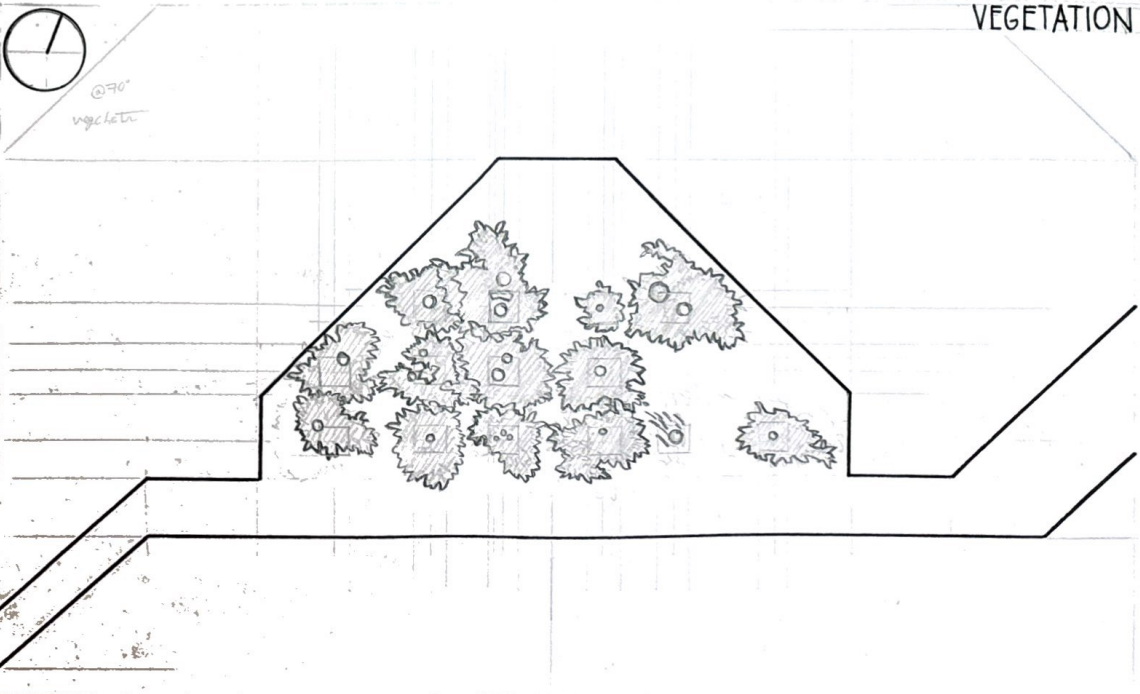
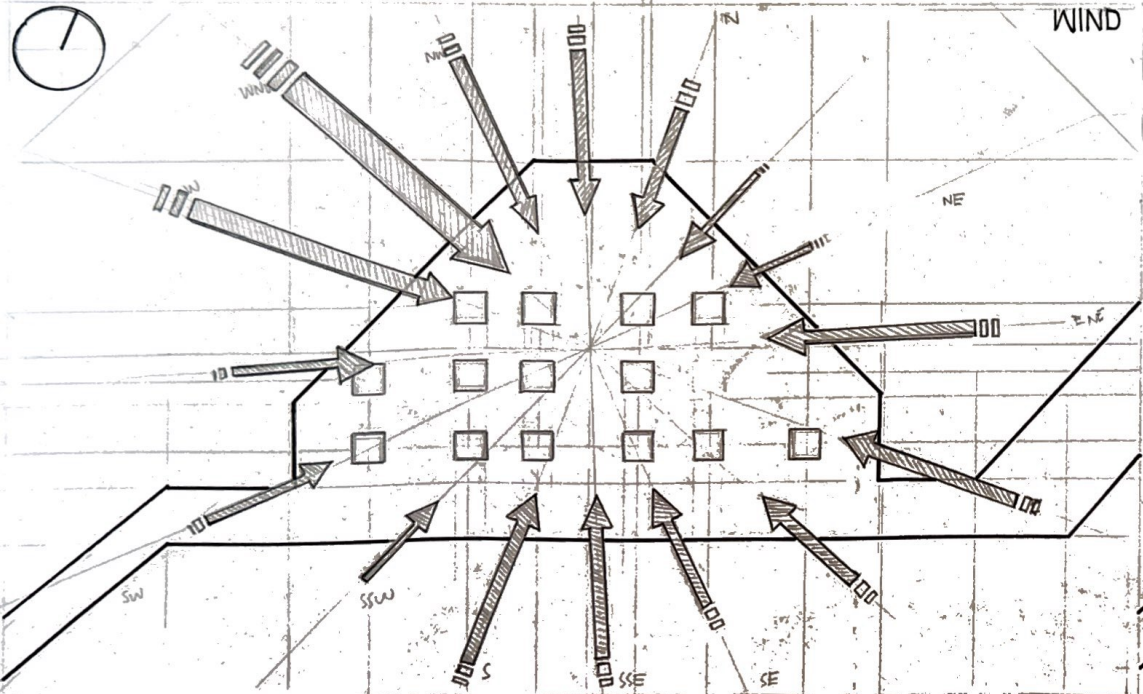


SITE'S PURPOSE

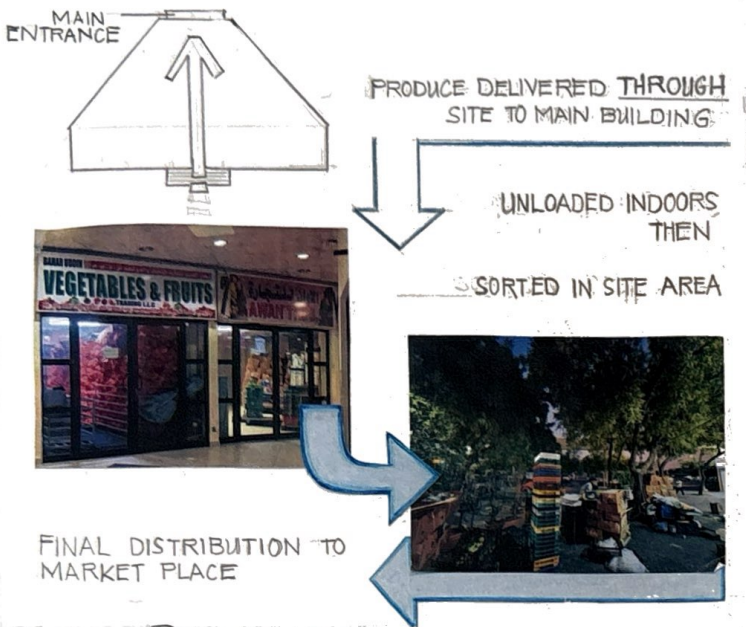



USER PRACTICES


SHOPS AT SITE'S PERIMETER INCLUDE :

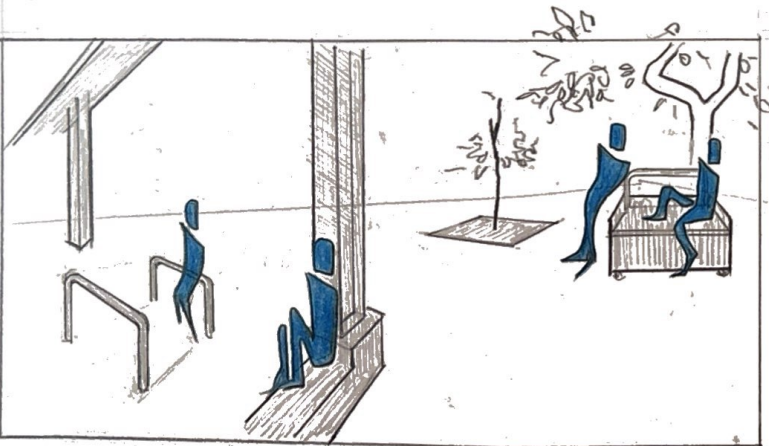
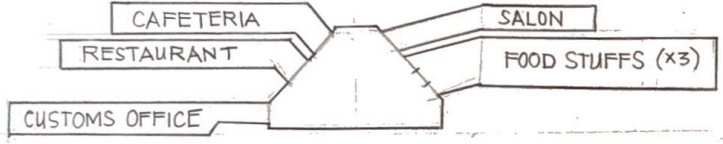



PROJECT DESIGN

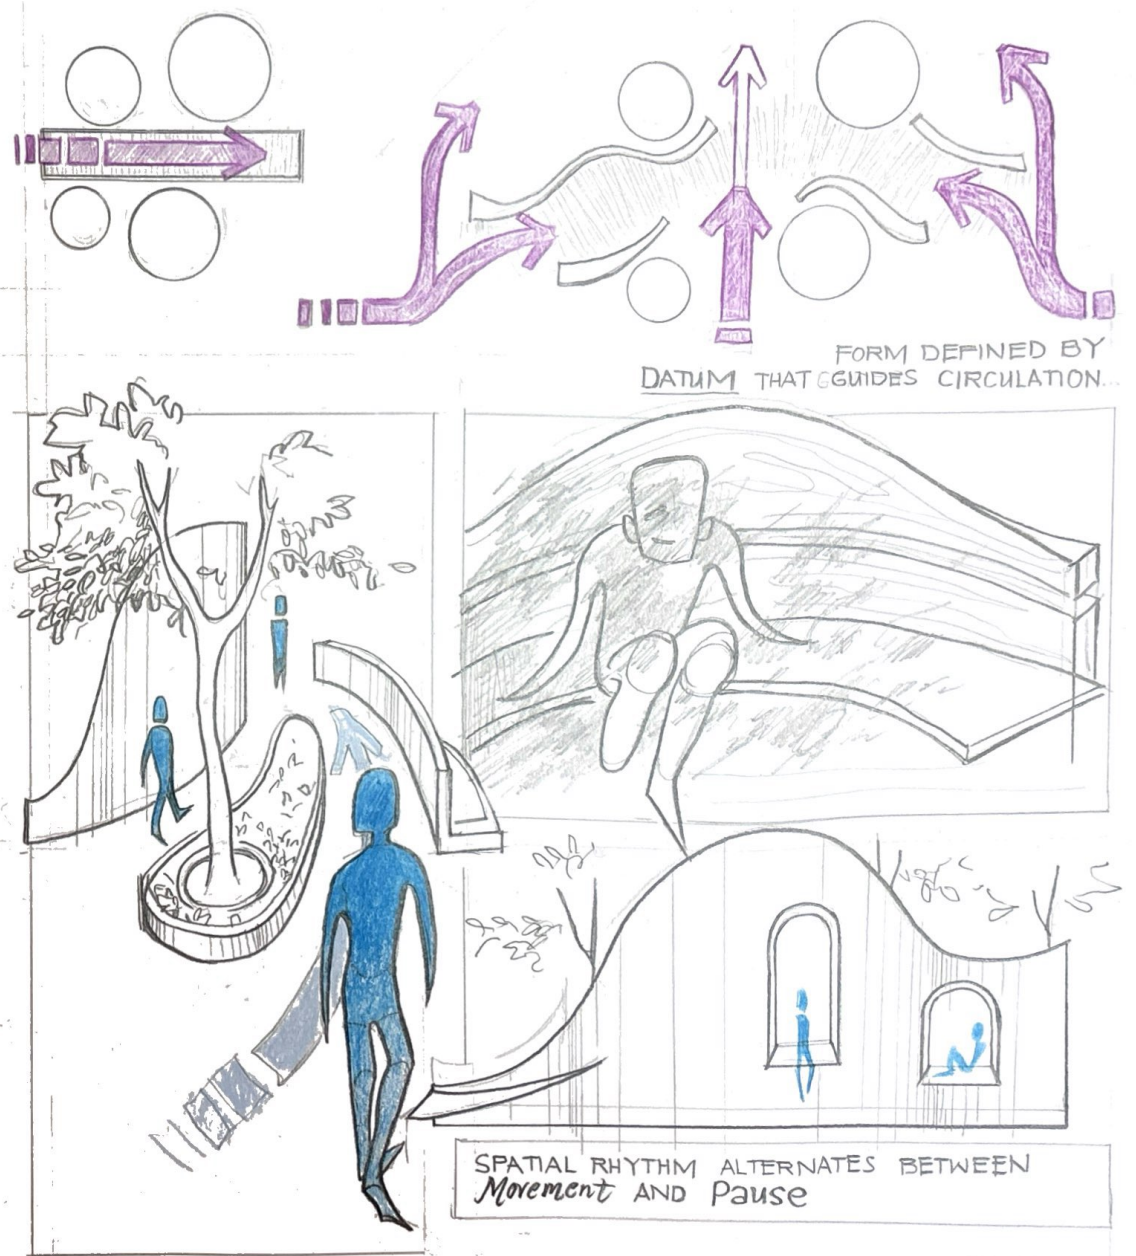

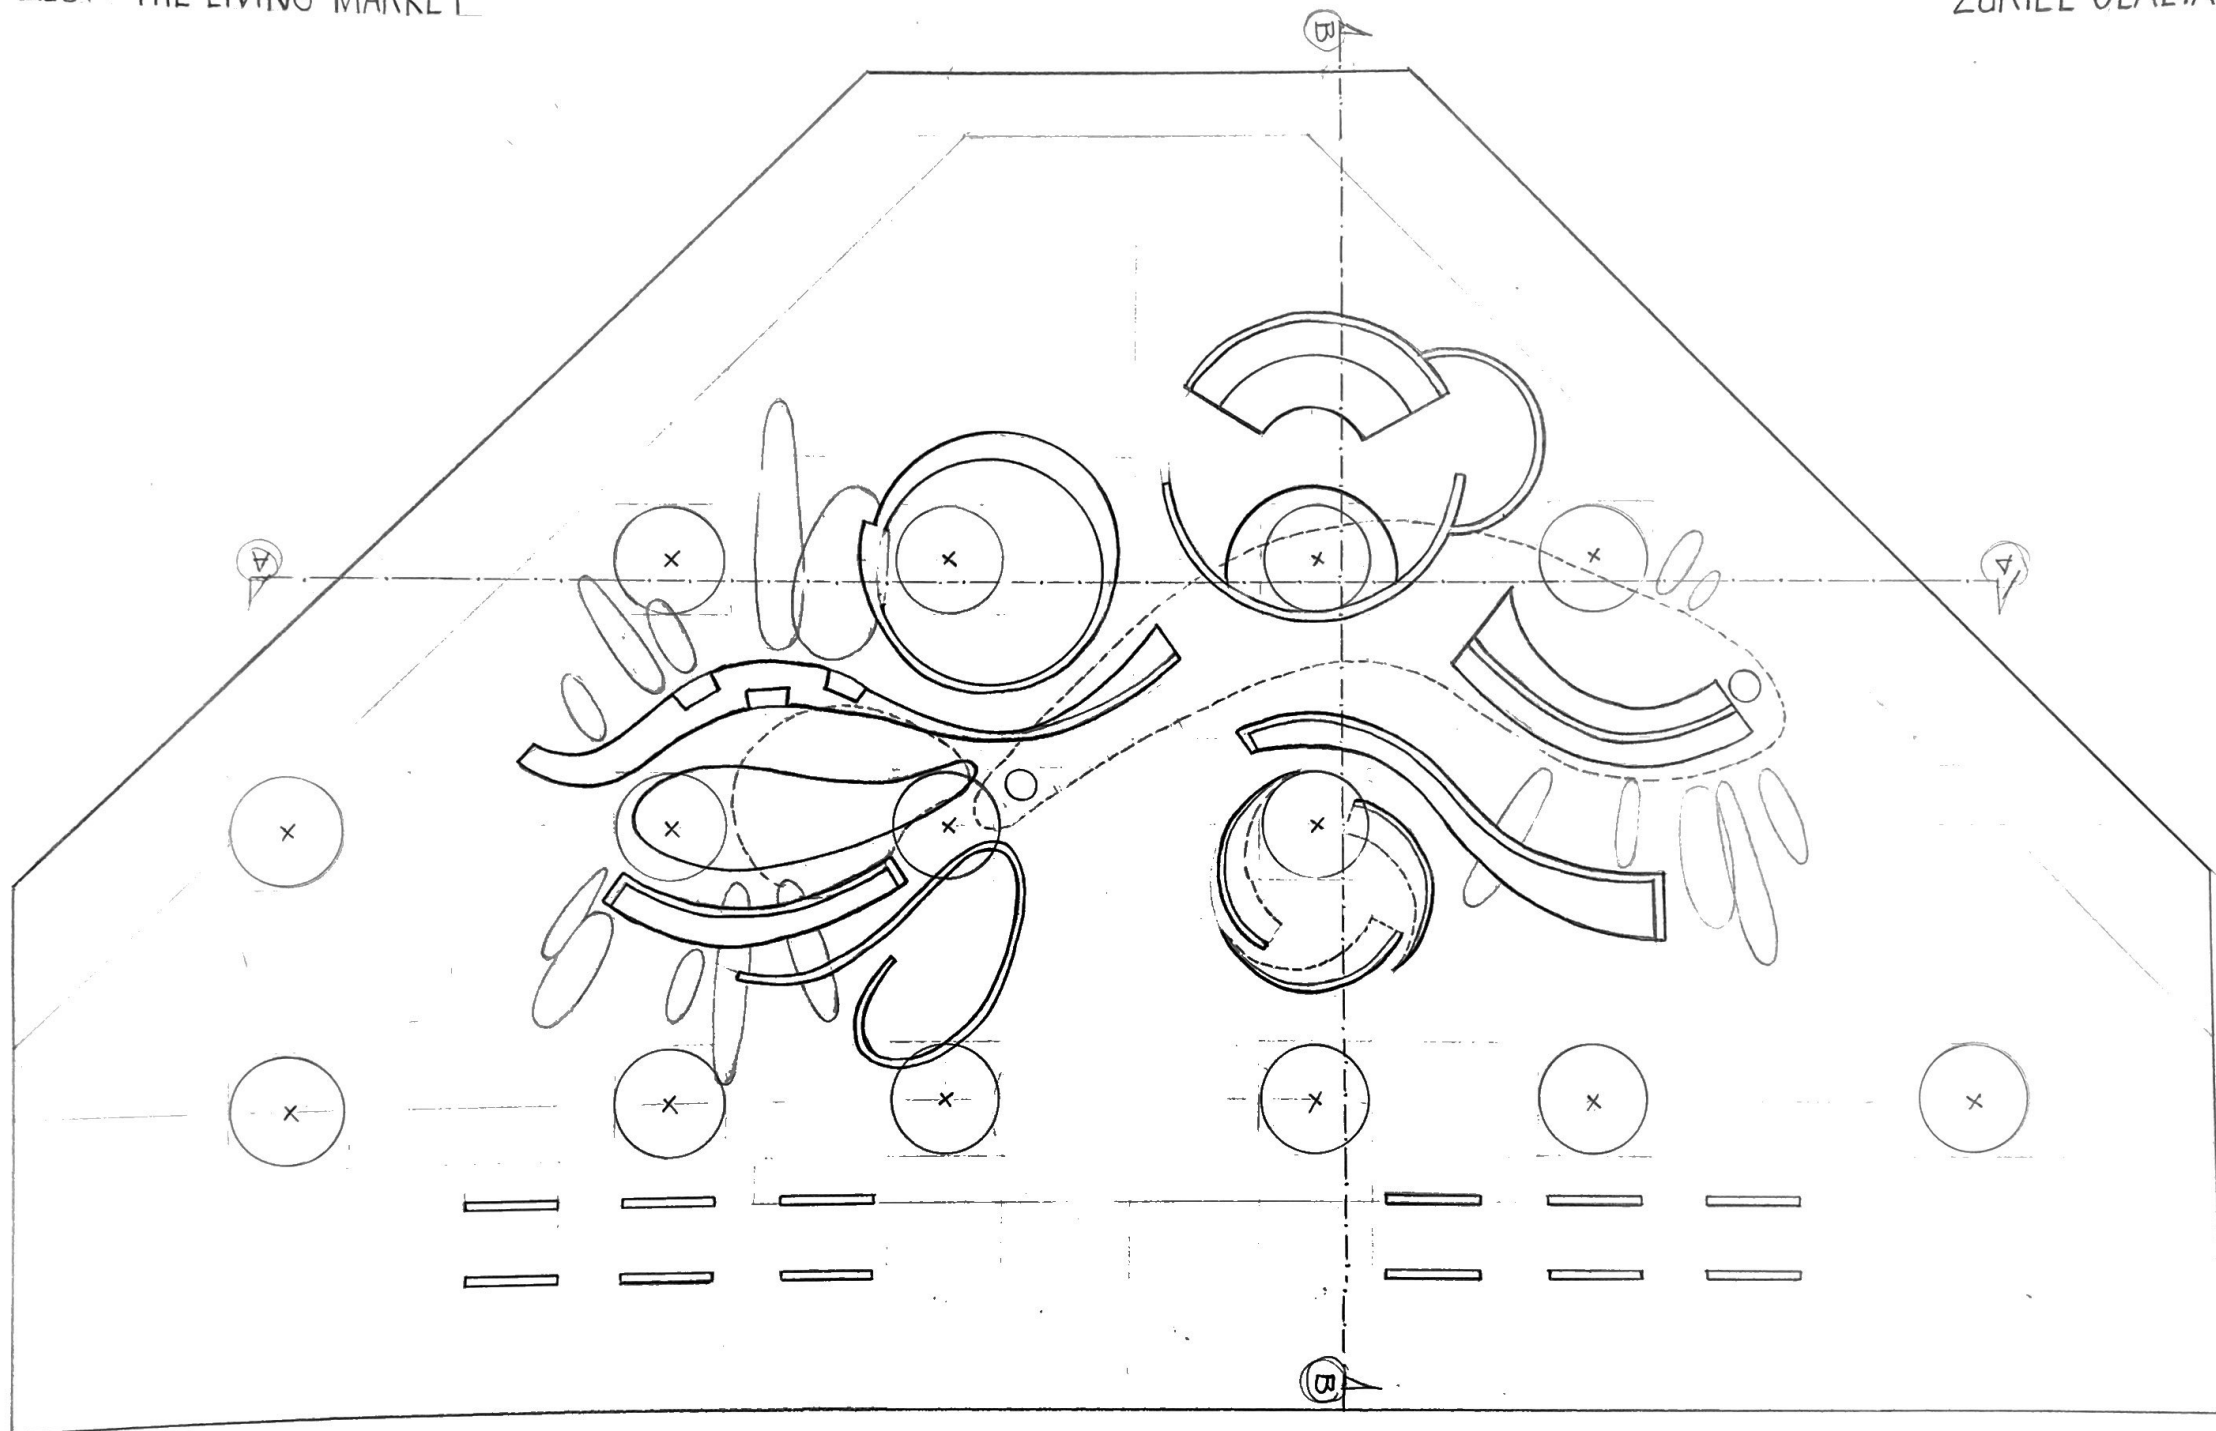


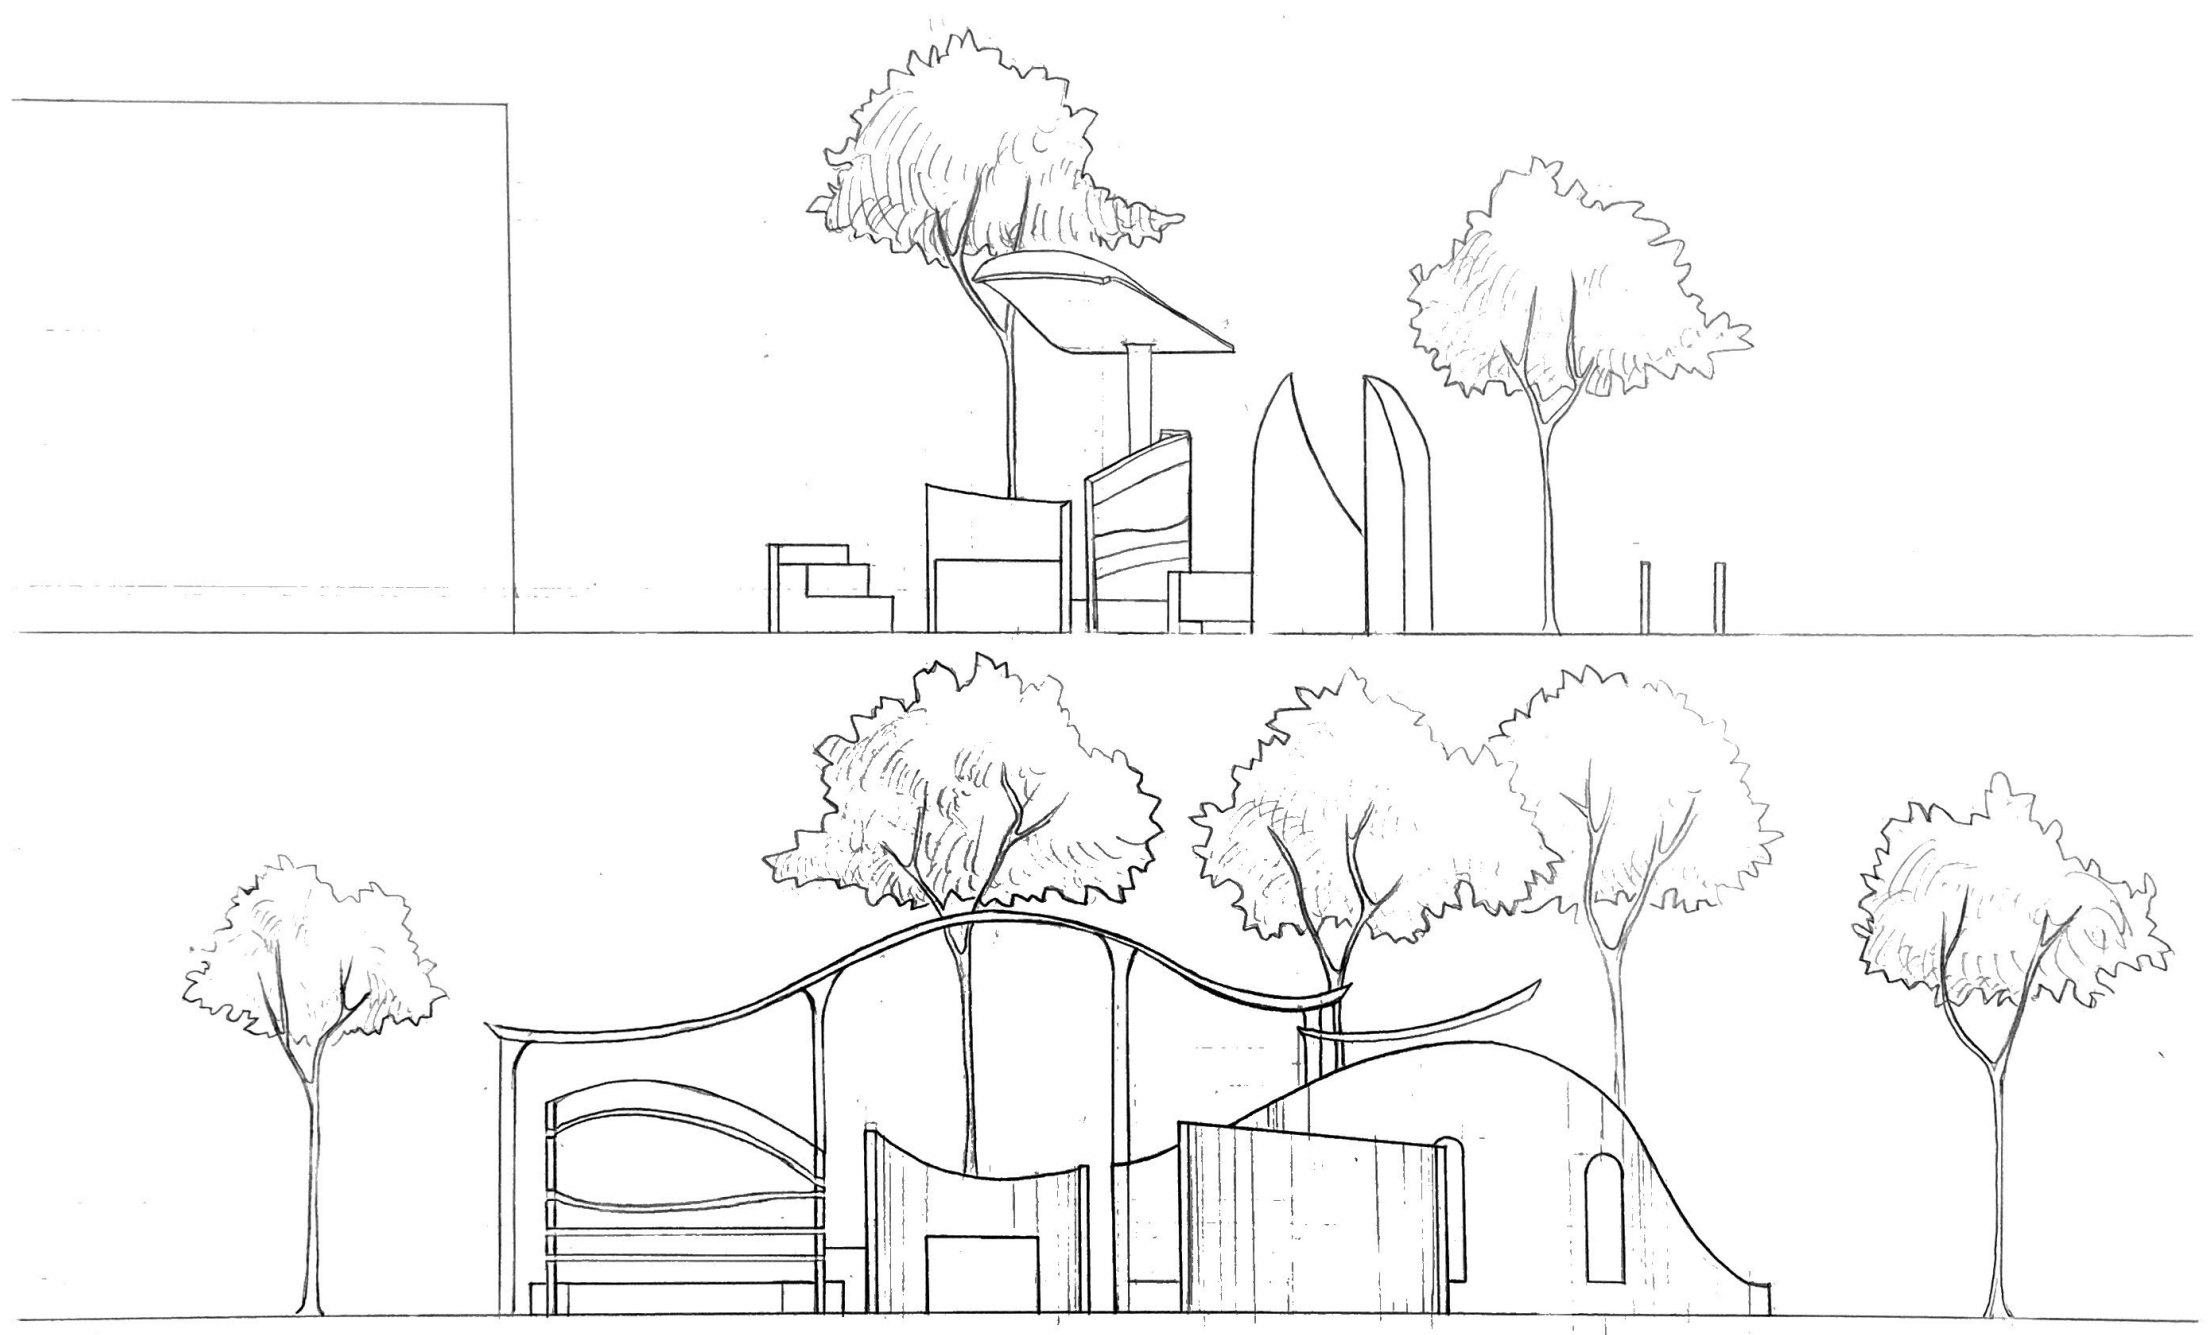

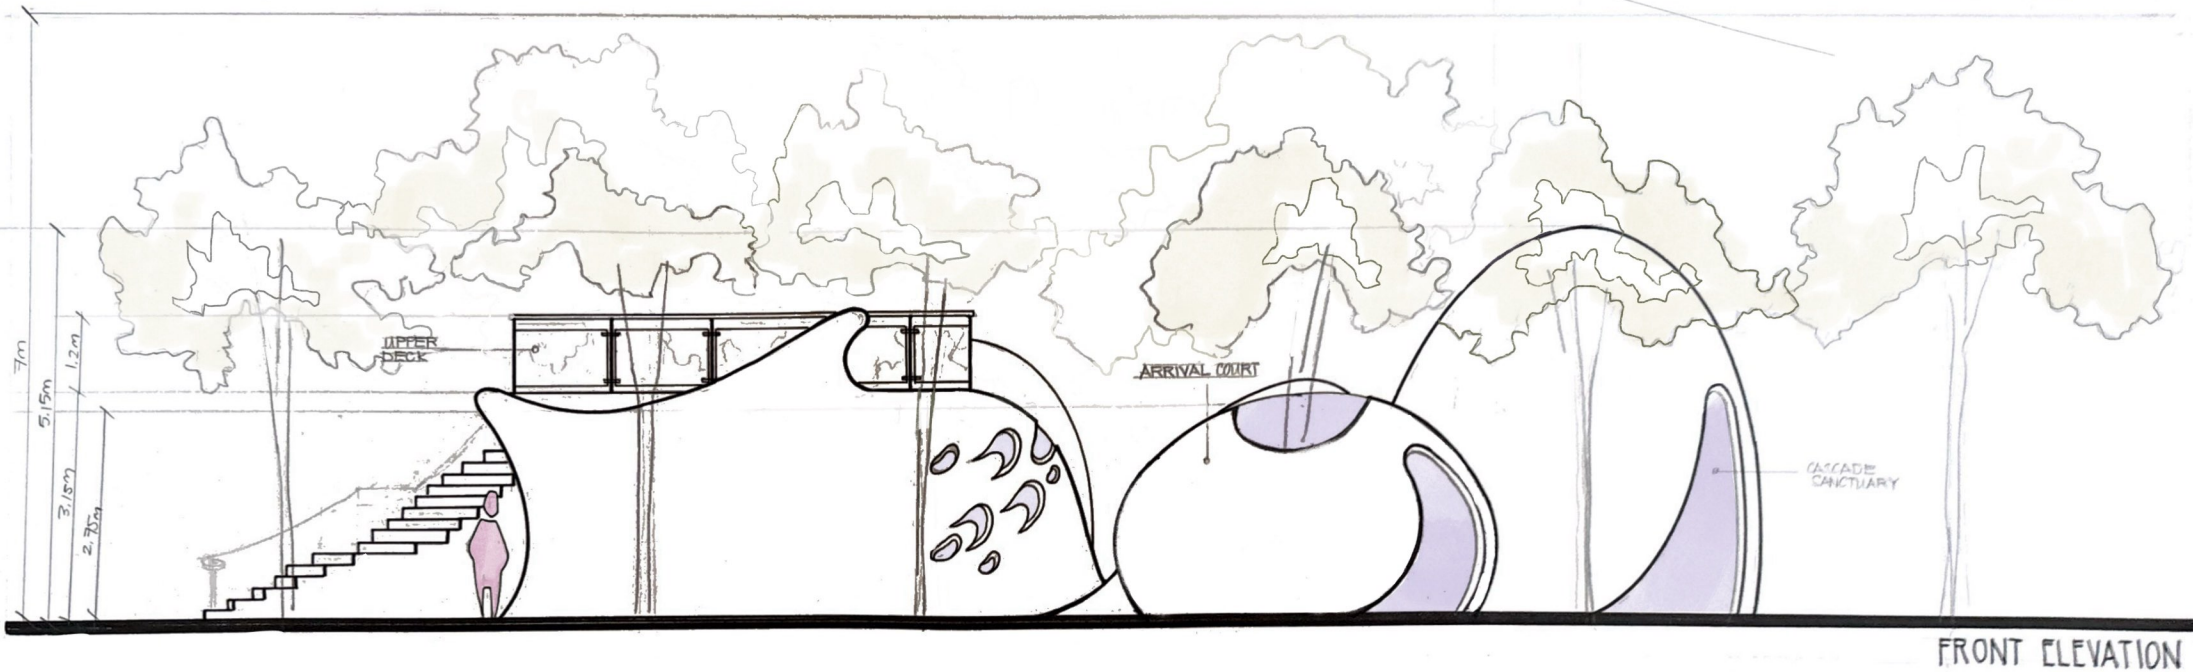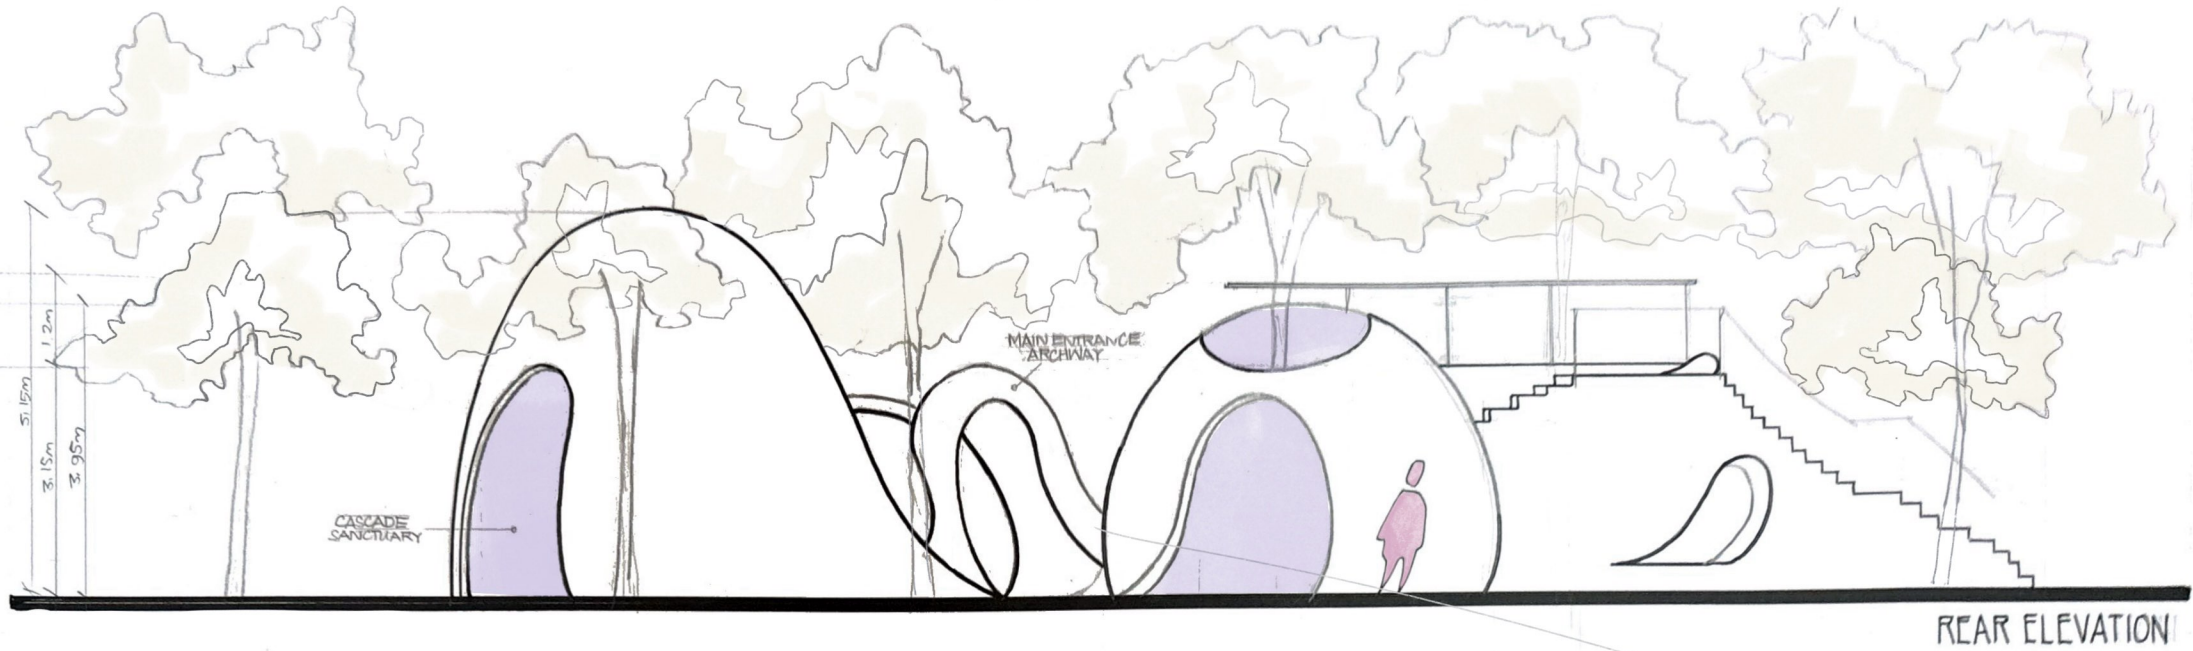


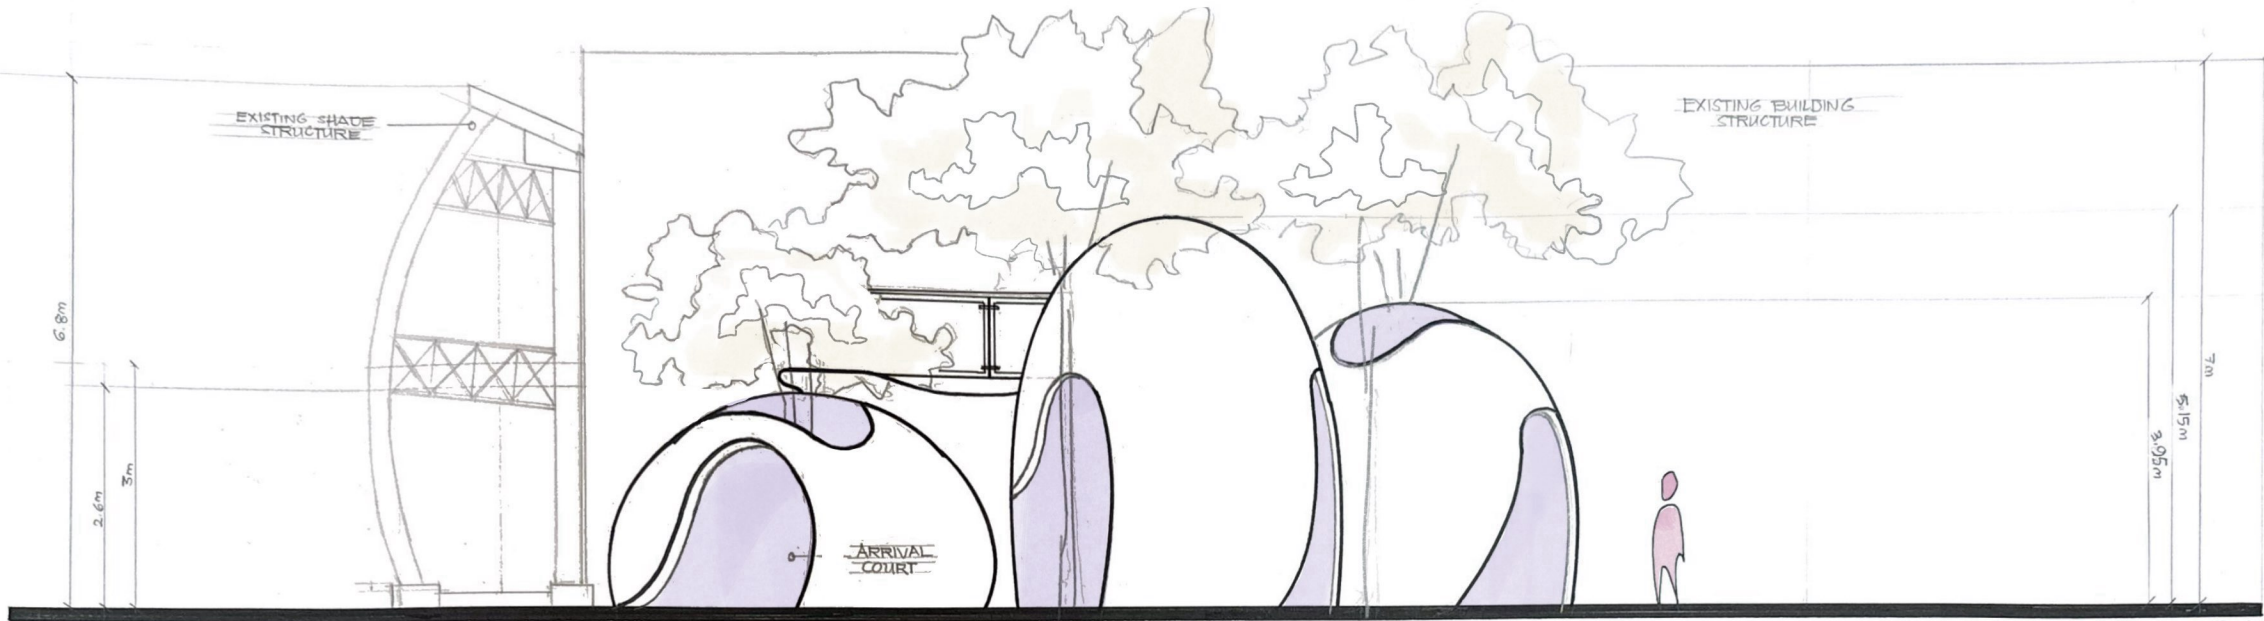


RIGHT-SIDE ELEVATION

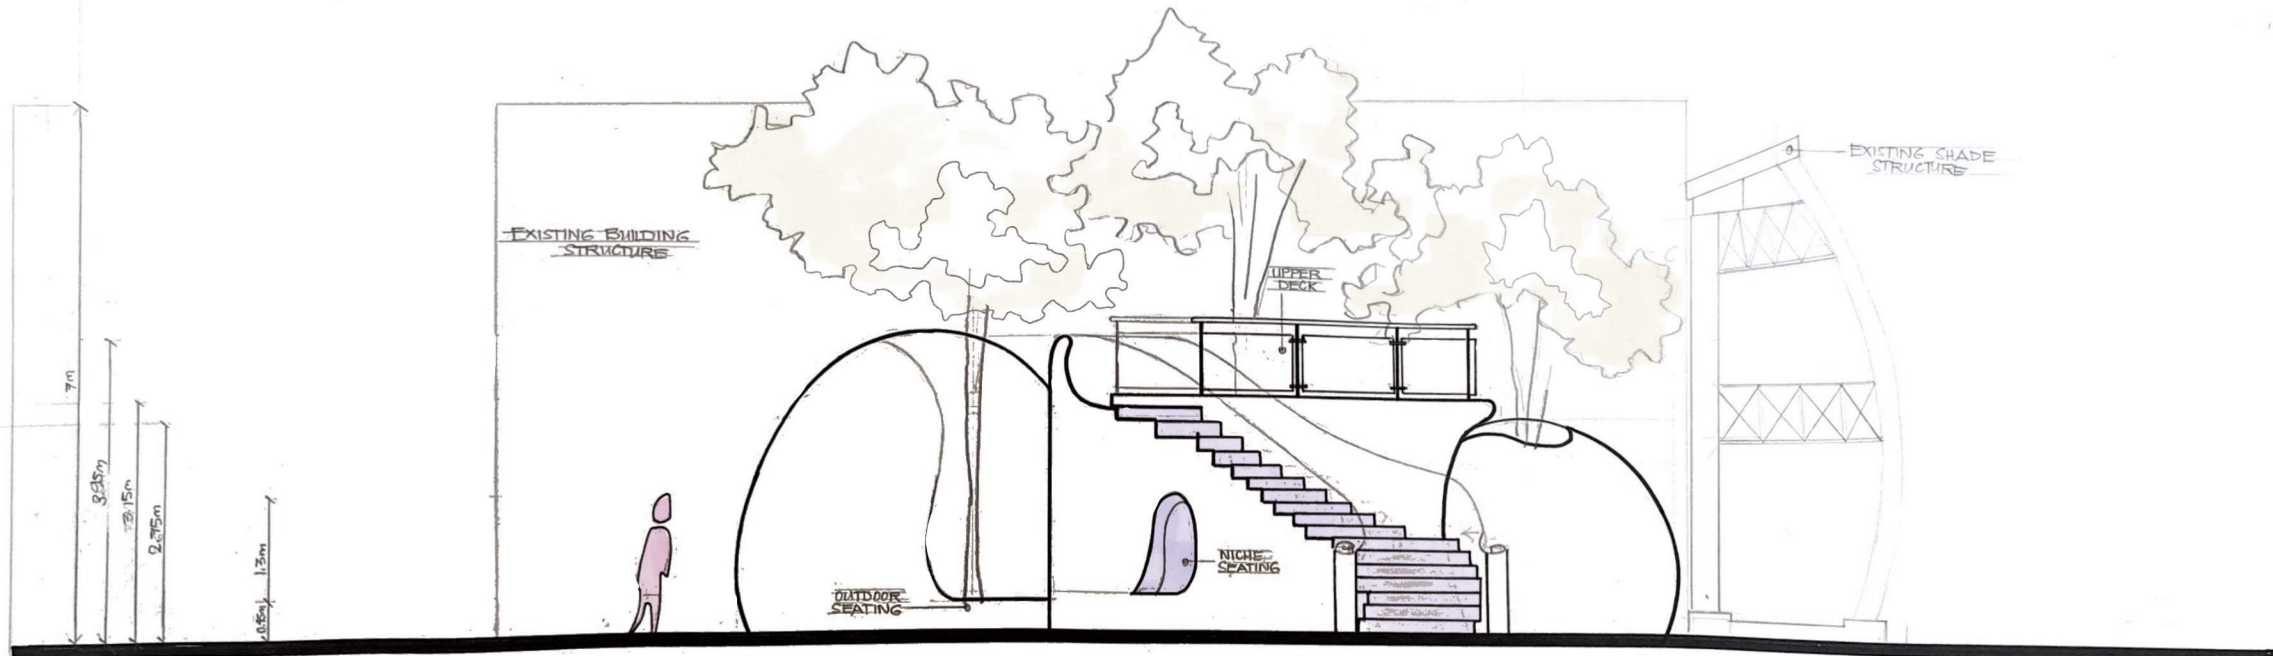








LEFT-SIDE ELEVATION


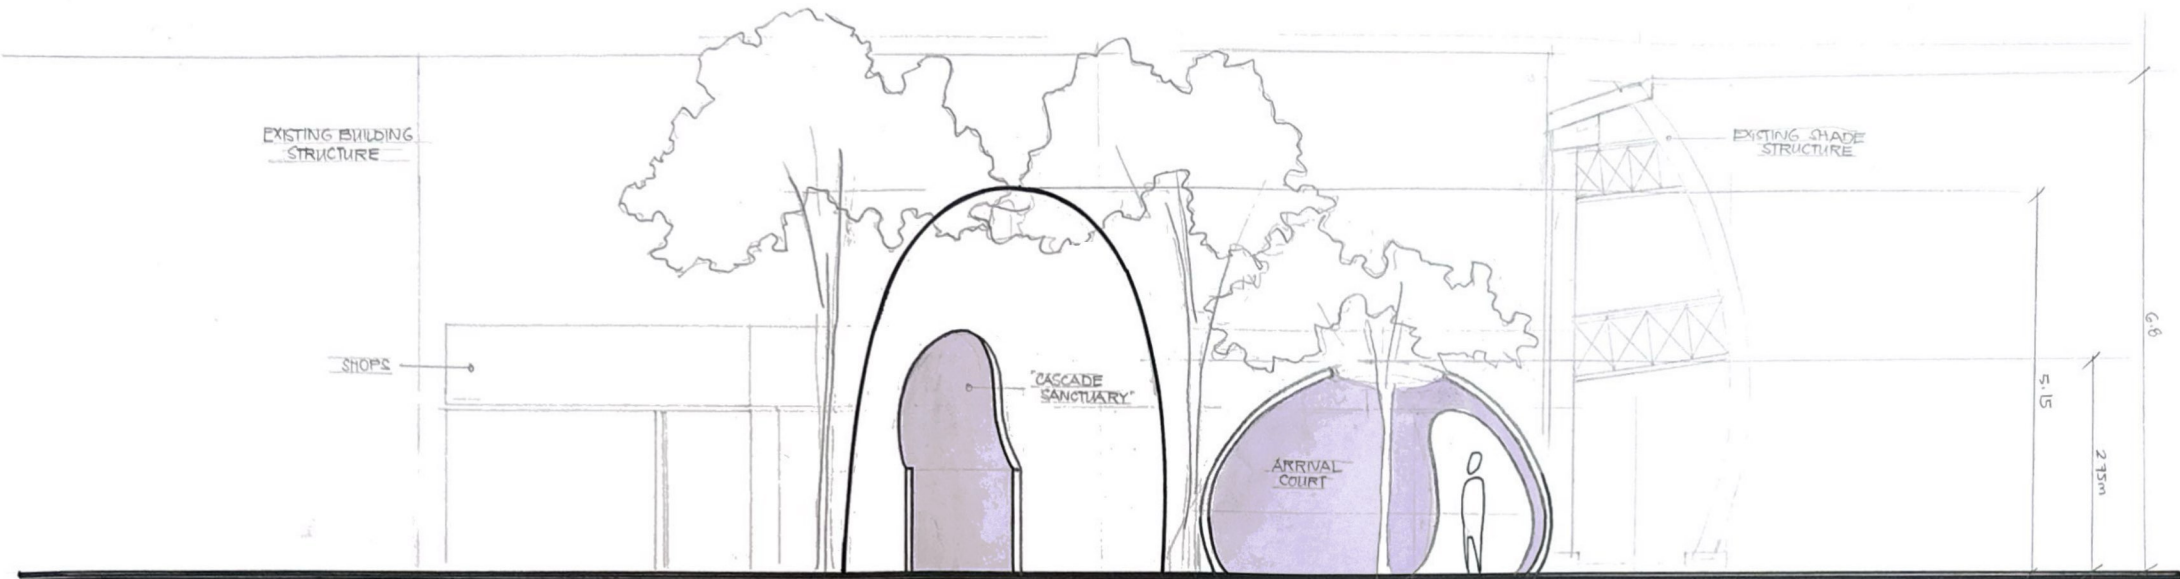





SECTION A-A

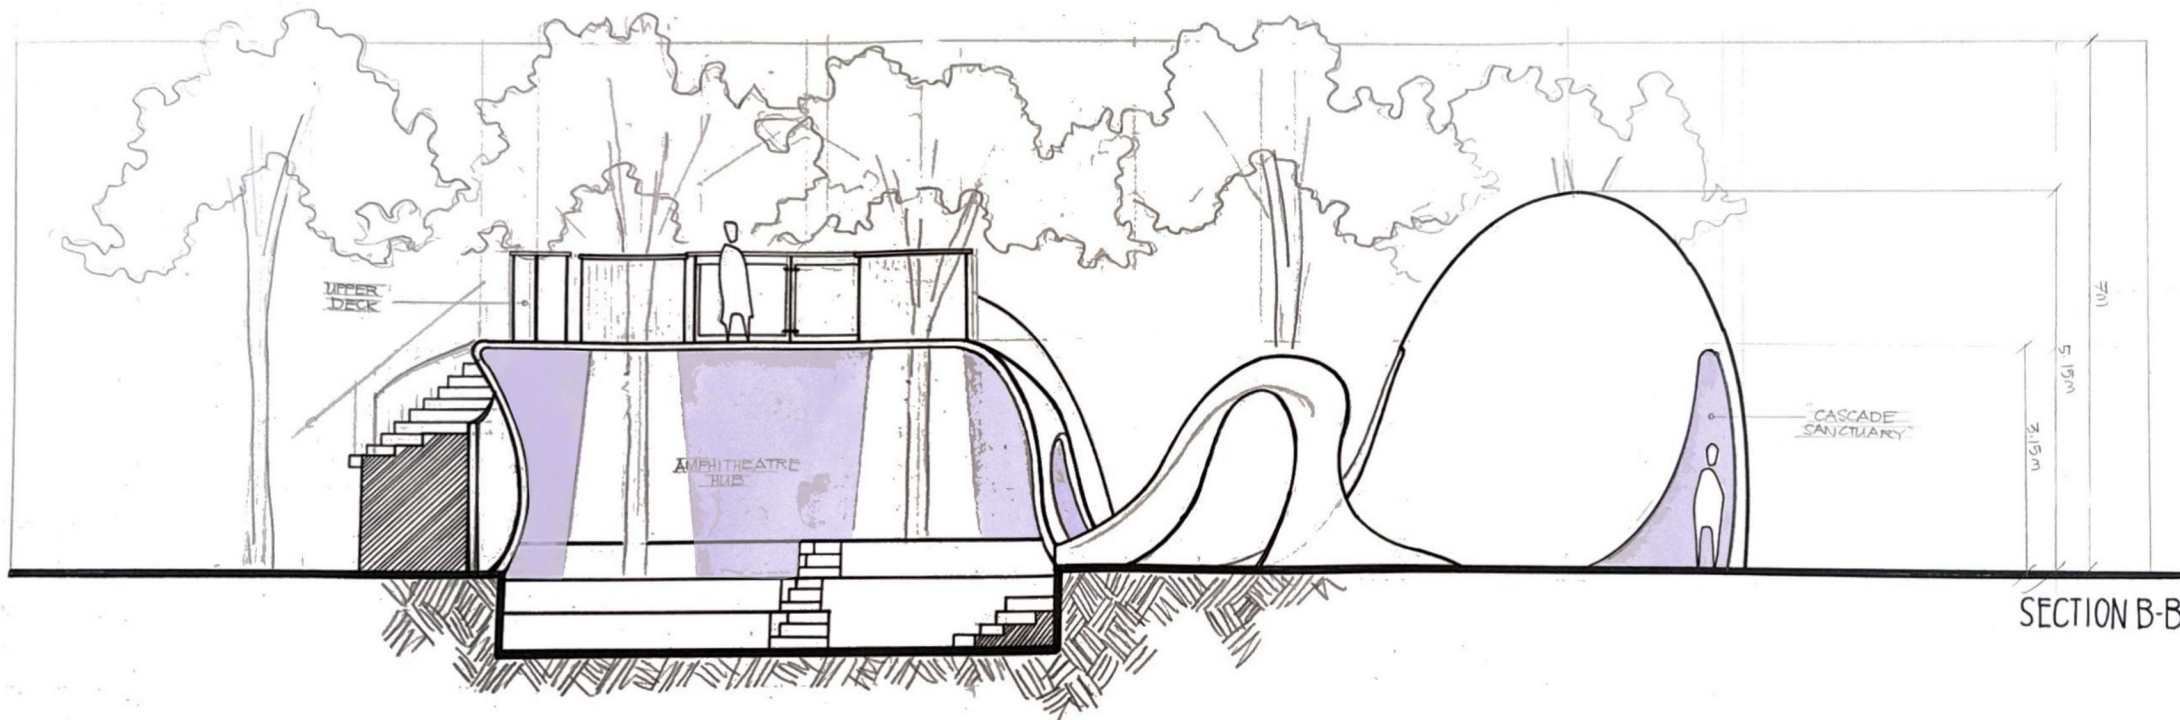



SECTION B-B

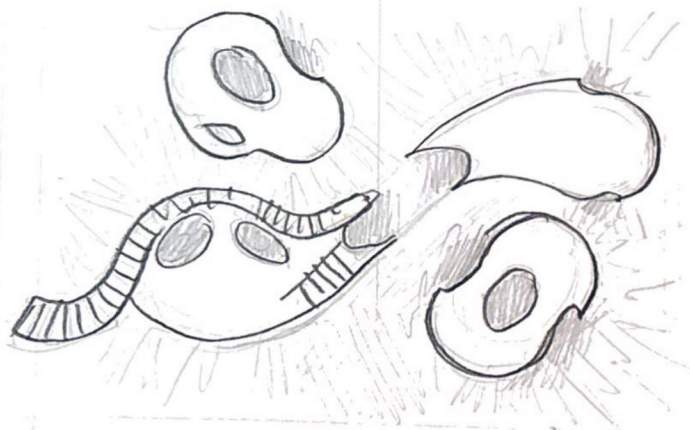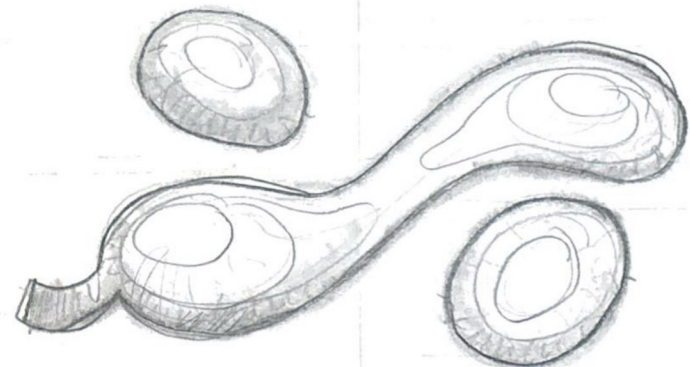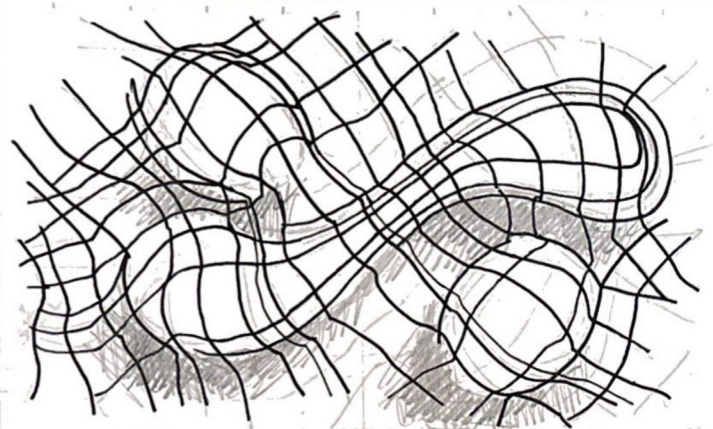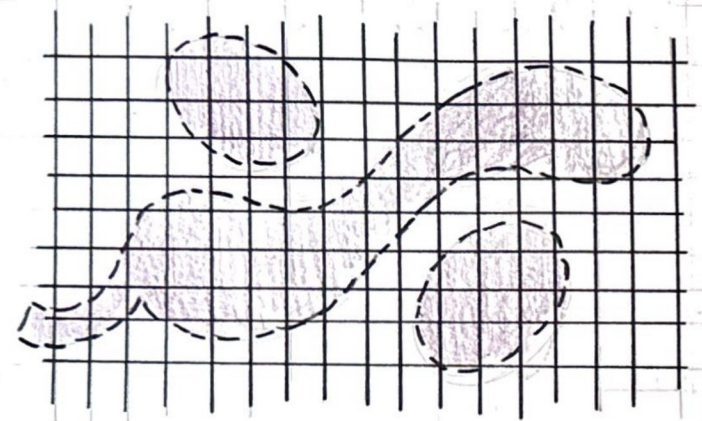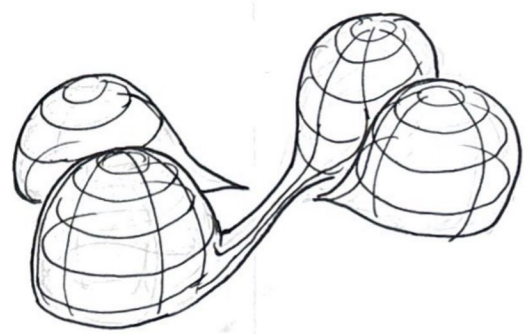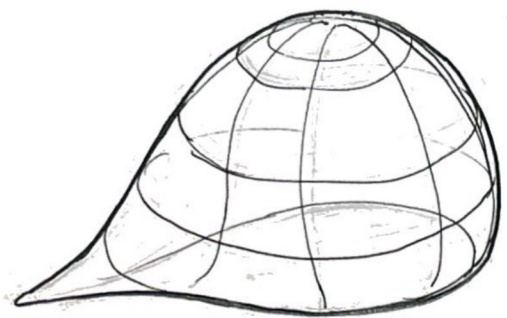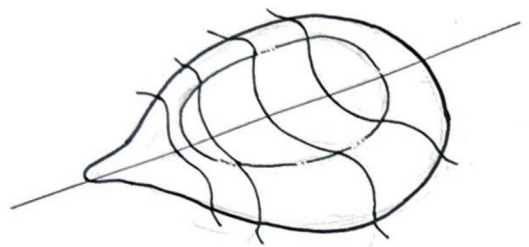

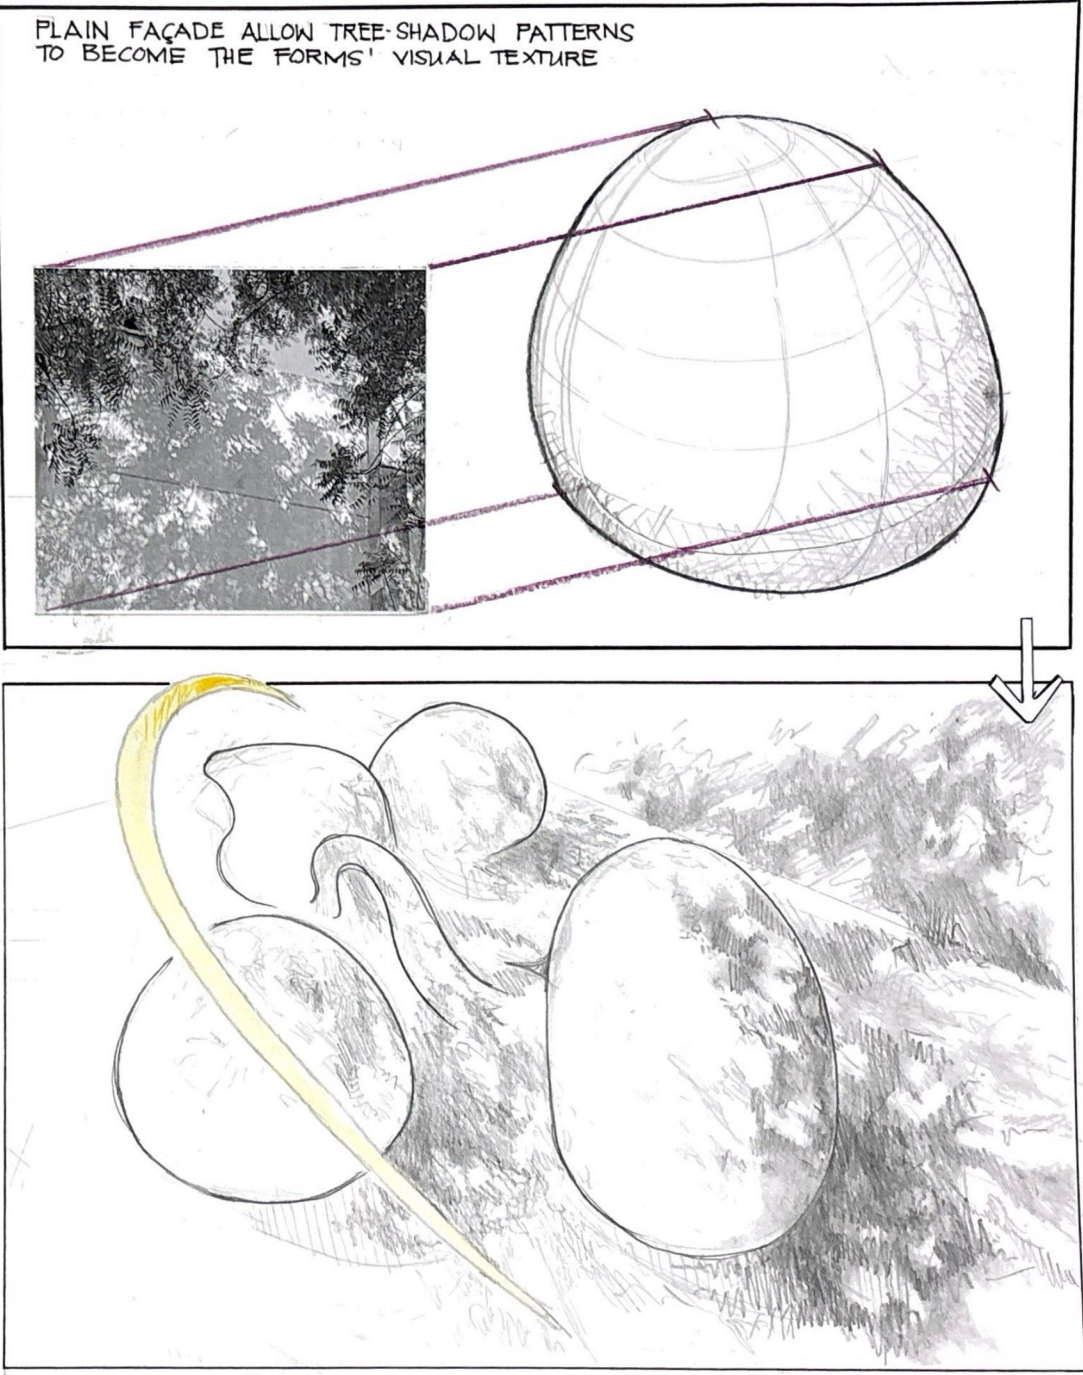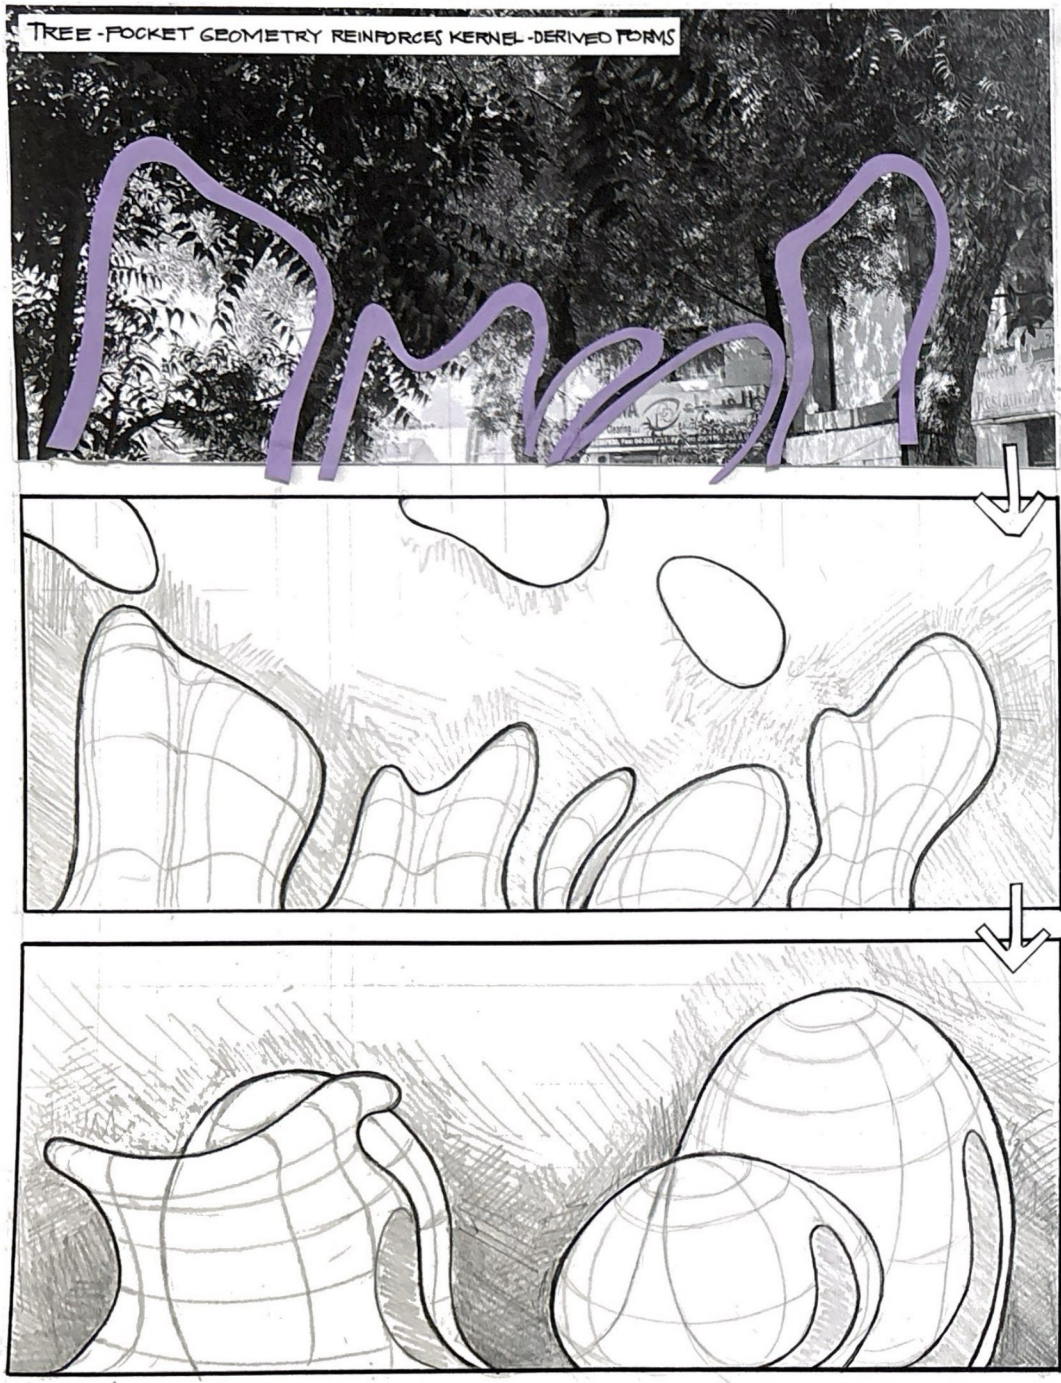

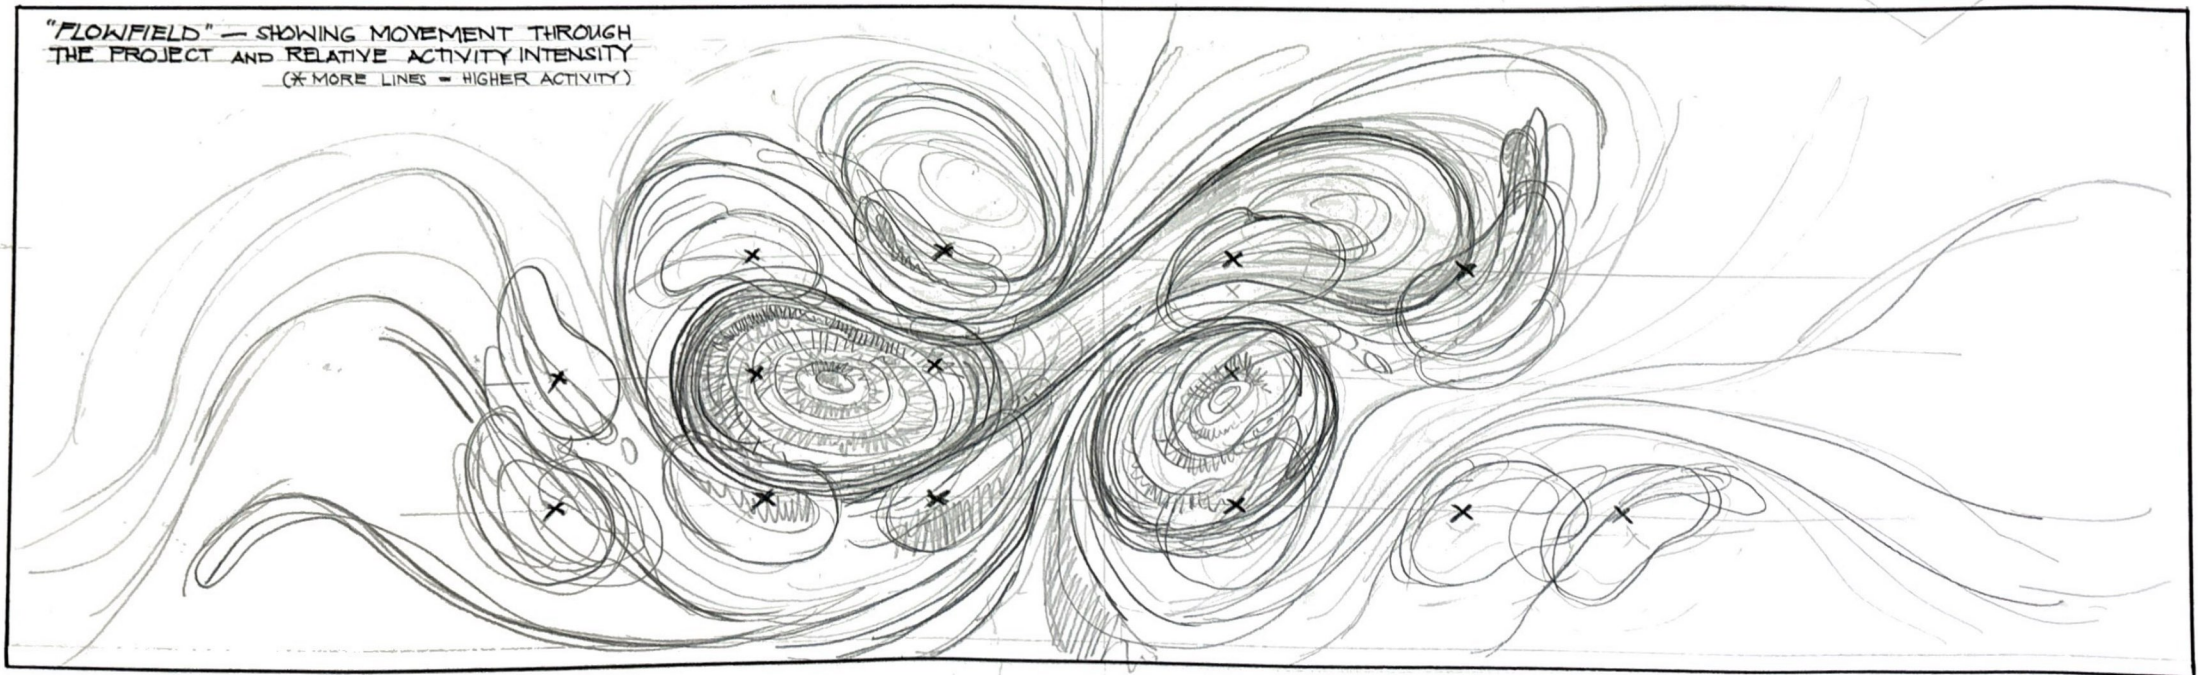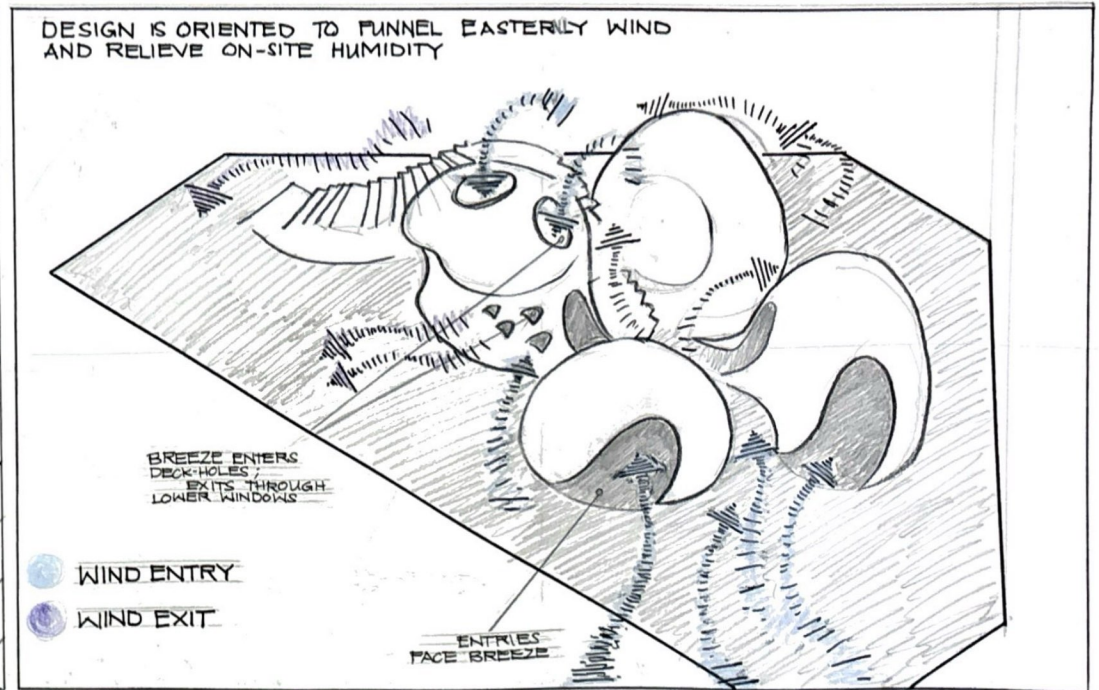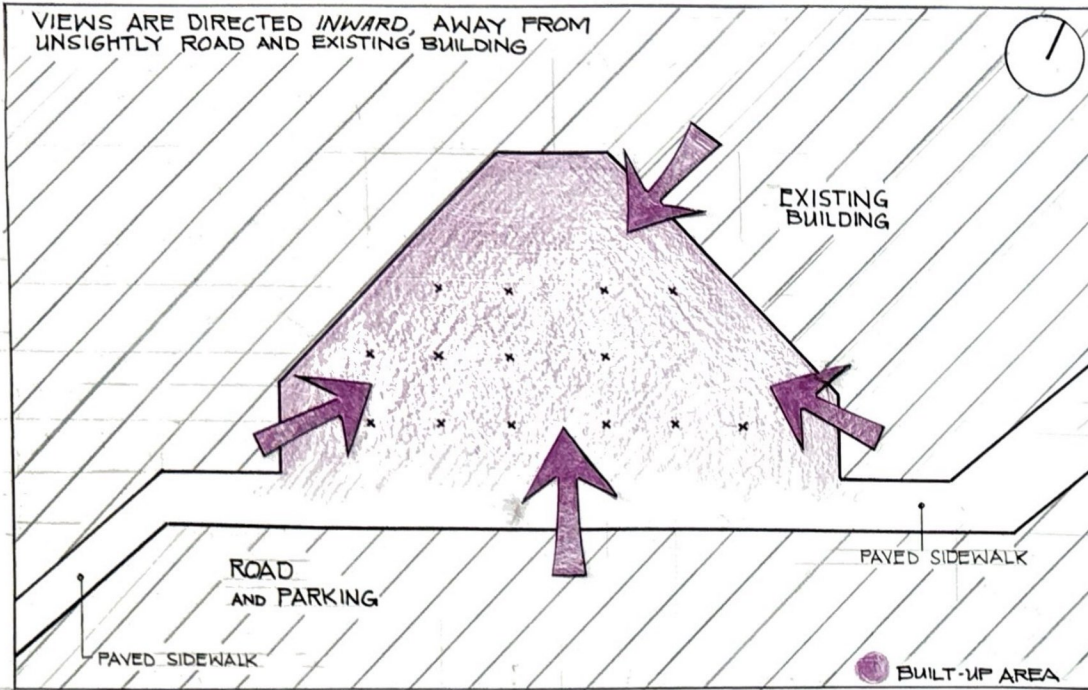

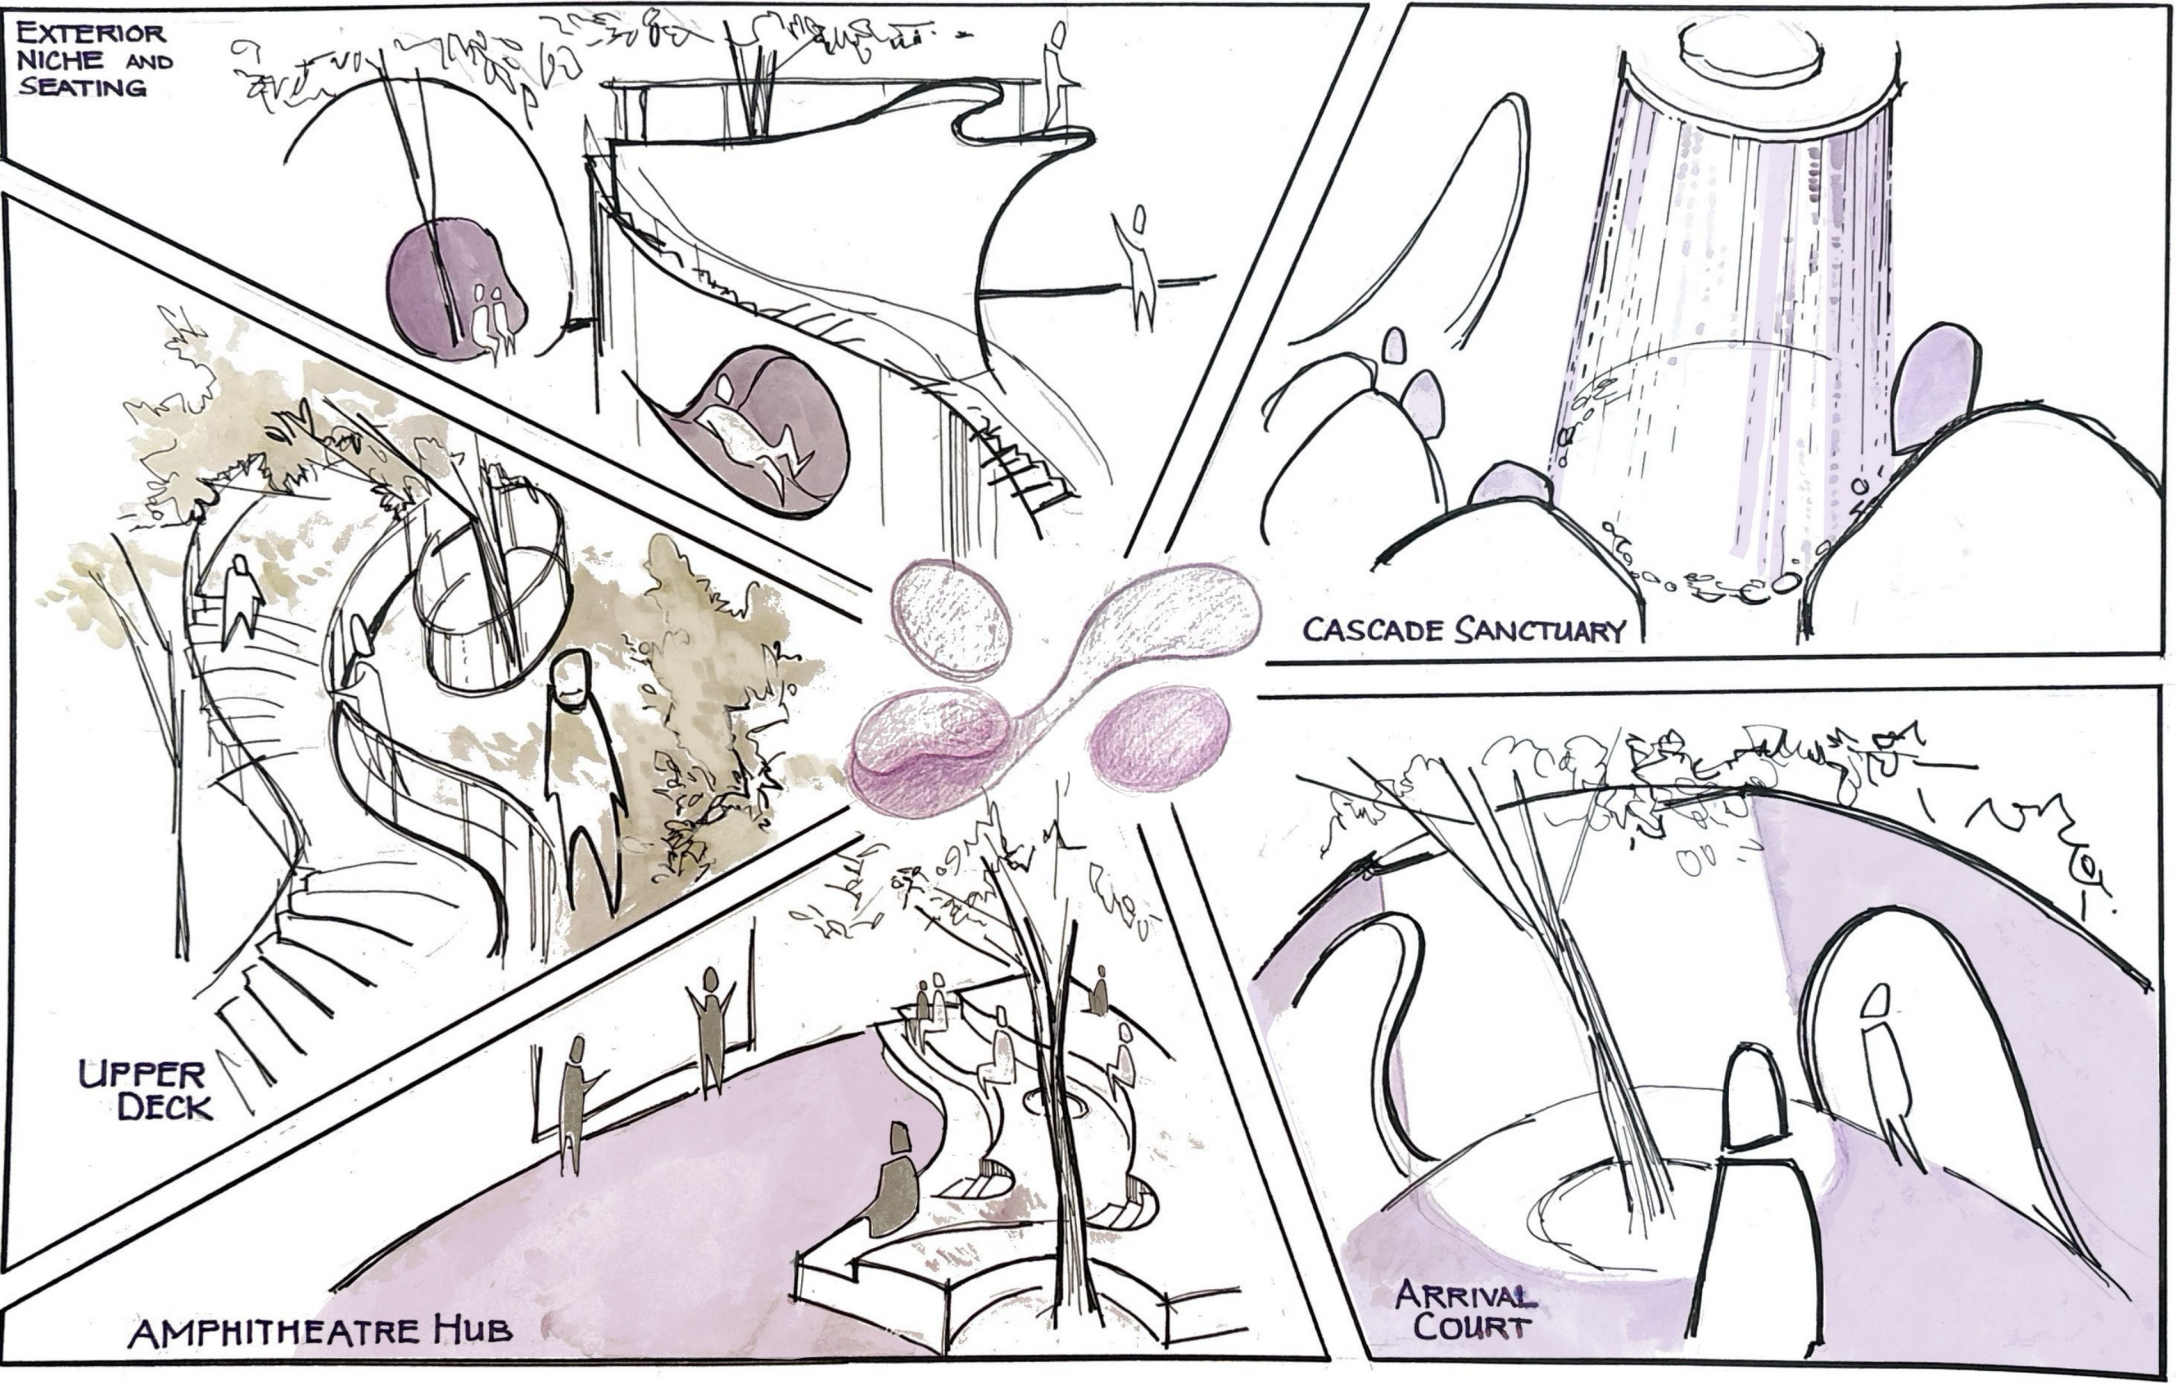

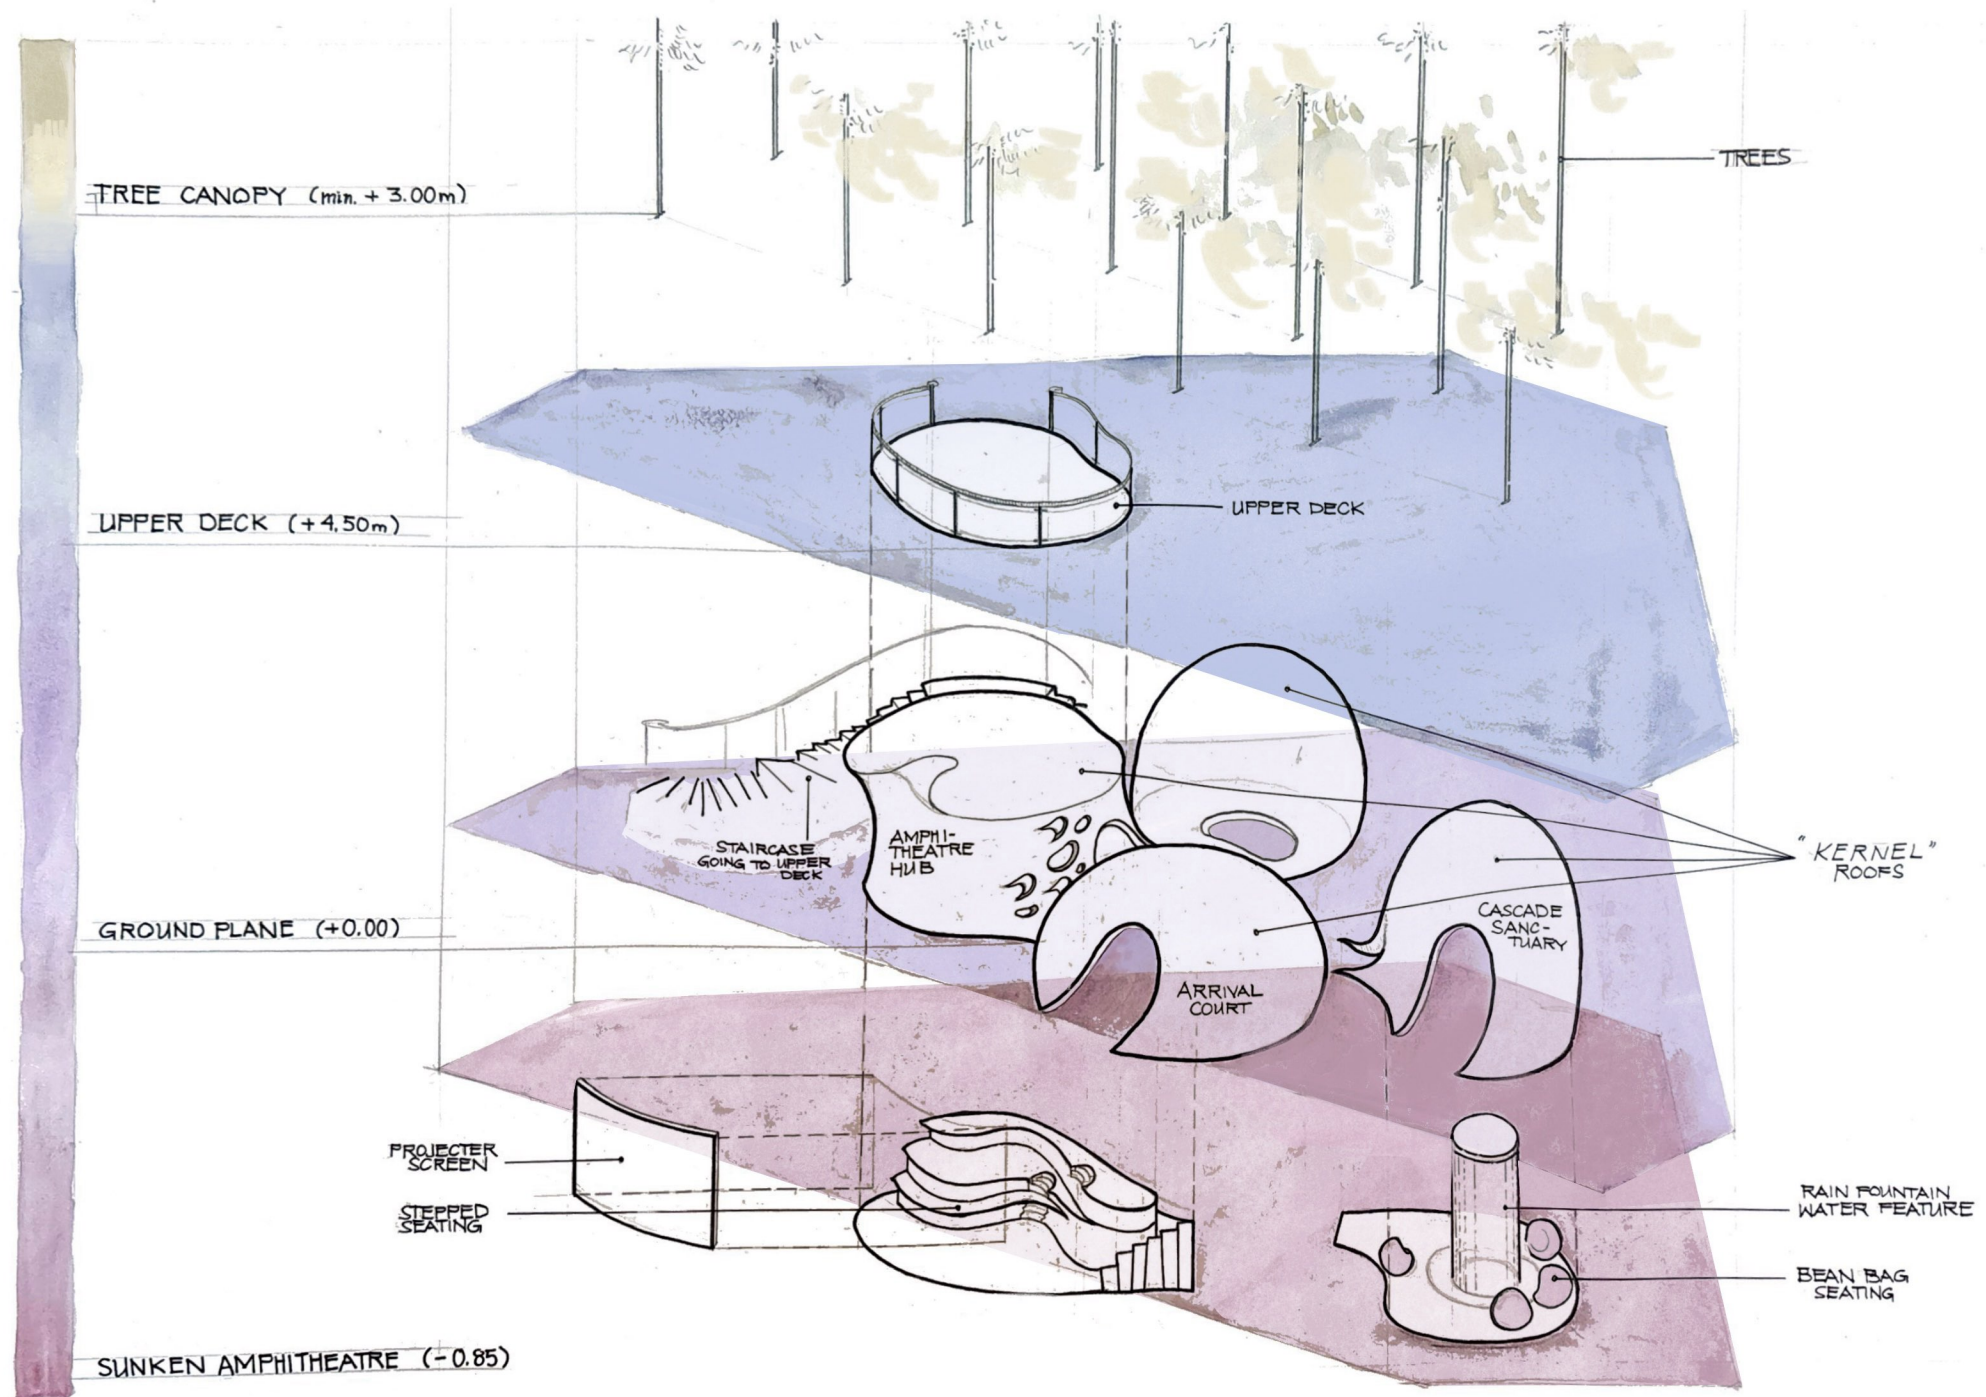



FRONT VIEW



AERIAL VIEW
AT RIGHT SIDE



LEFT SIDE



RIGHT SIDE VIEW



REAR SIDE VIEW



TOP VIEW



AXONOMETRIC VIEW



TOP VIEW SHOWING LOWER LEVEL



AXONOMETRIC SHOWING LOWER LEVEL




NIGHT SCENE (FRONT VIEW)





NIGHT SCENE (RIGHT SIDE VIEW)



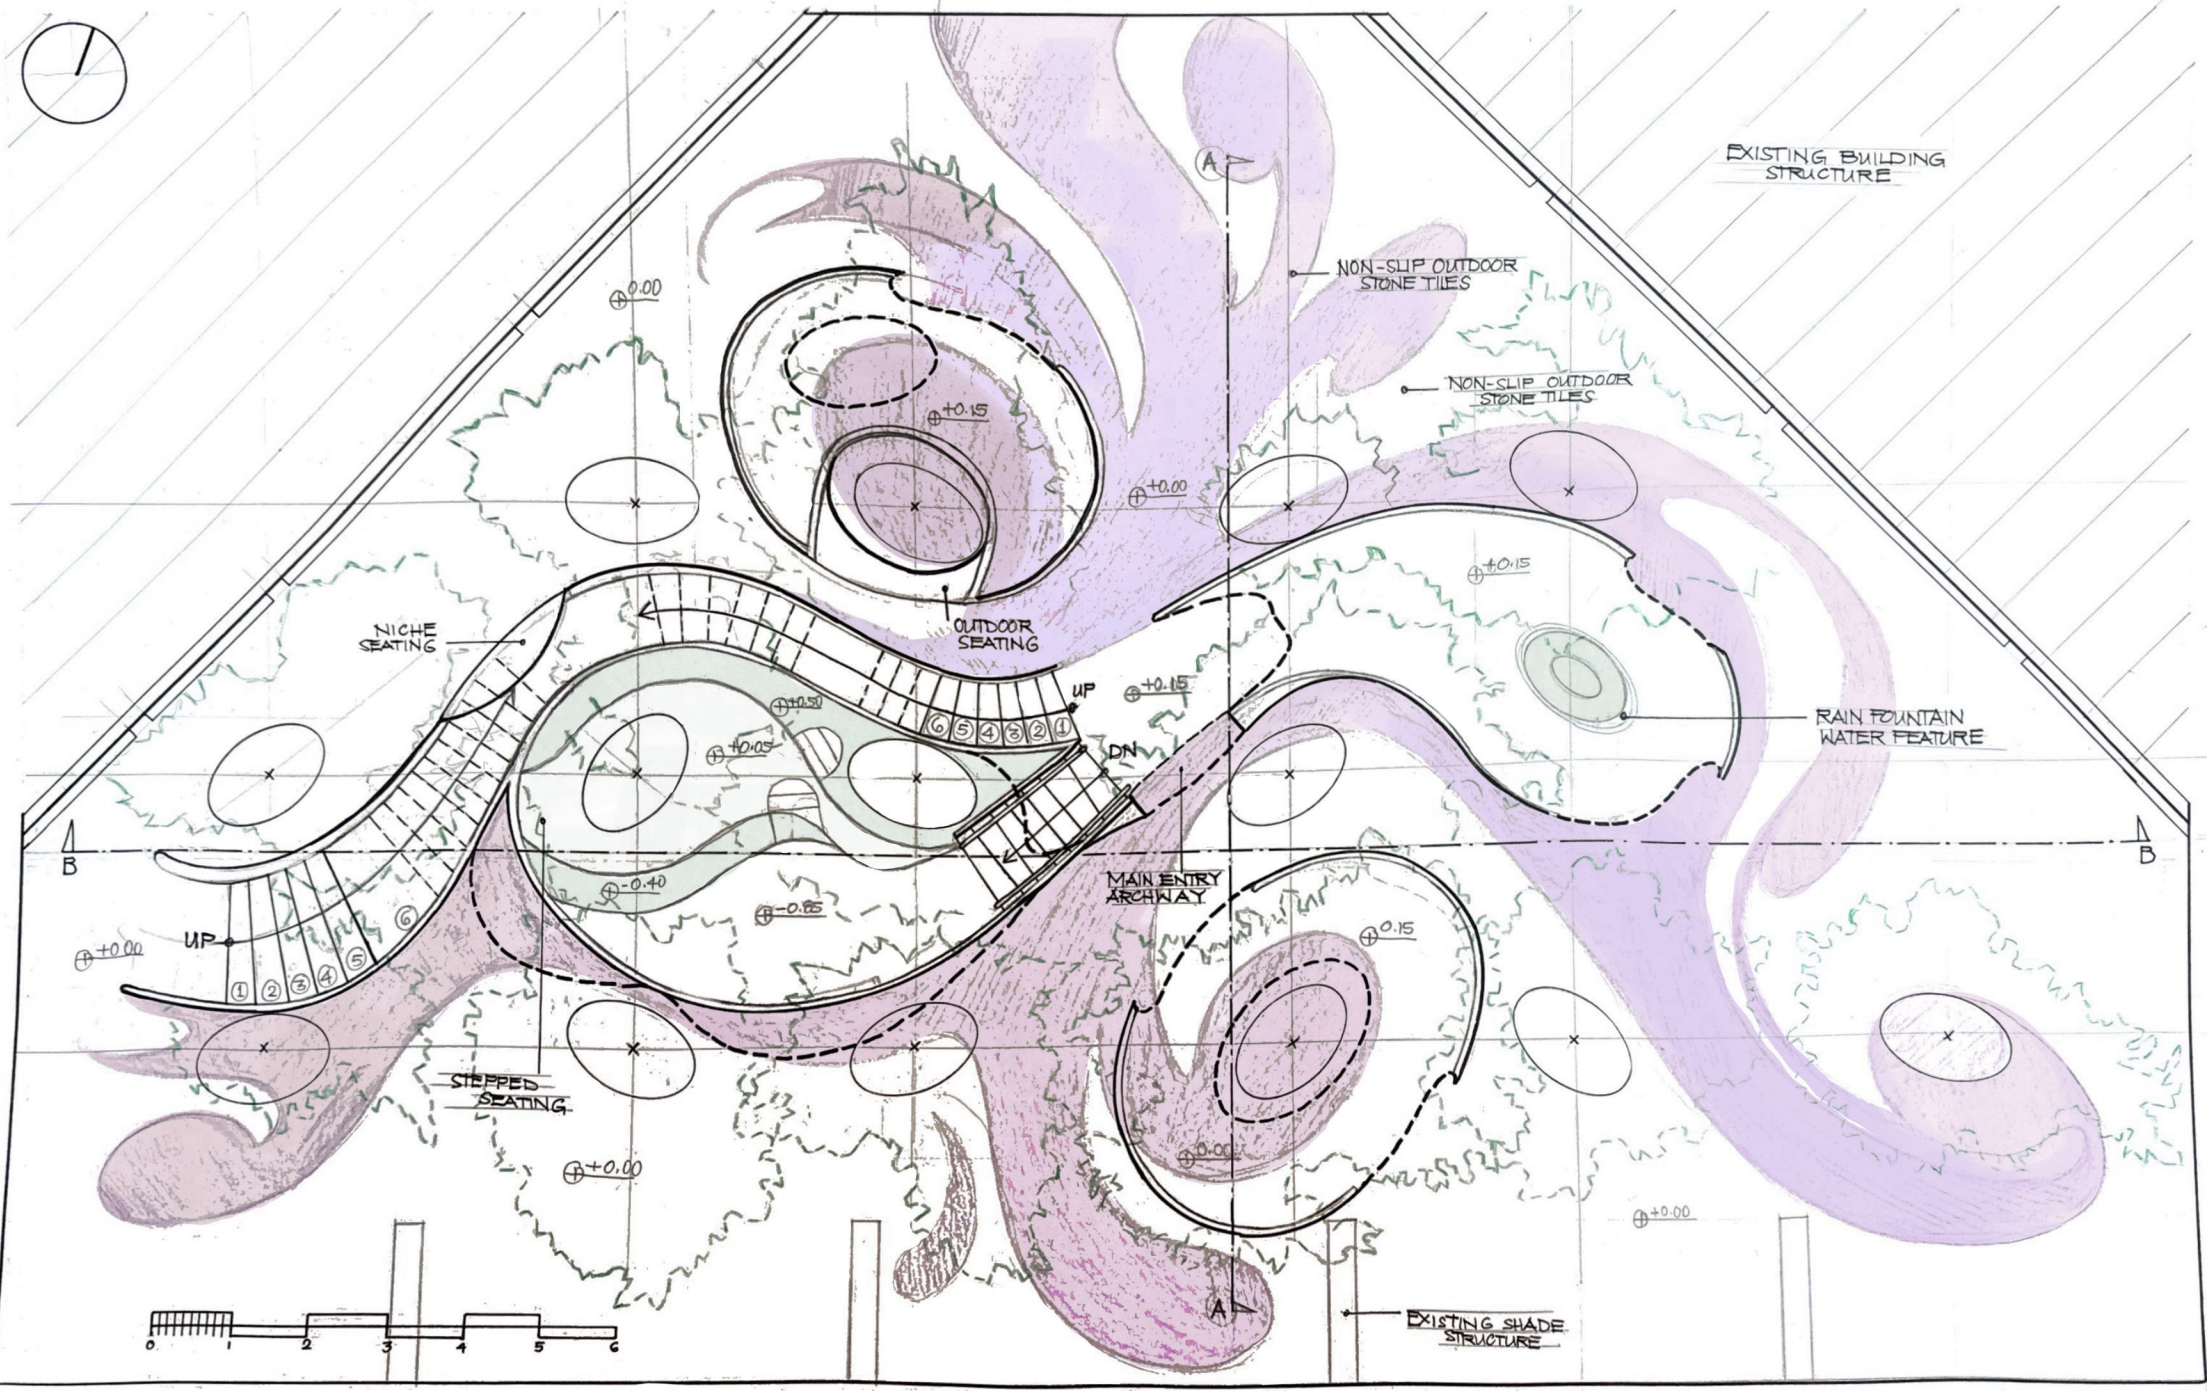

PHASE 3 - ARCHITECTURE - GROUND FLOOR PLAN (1:50)

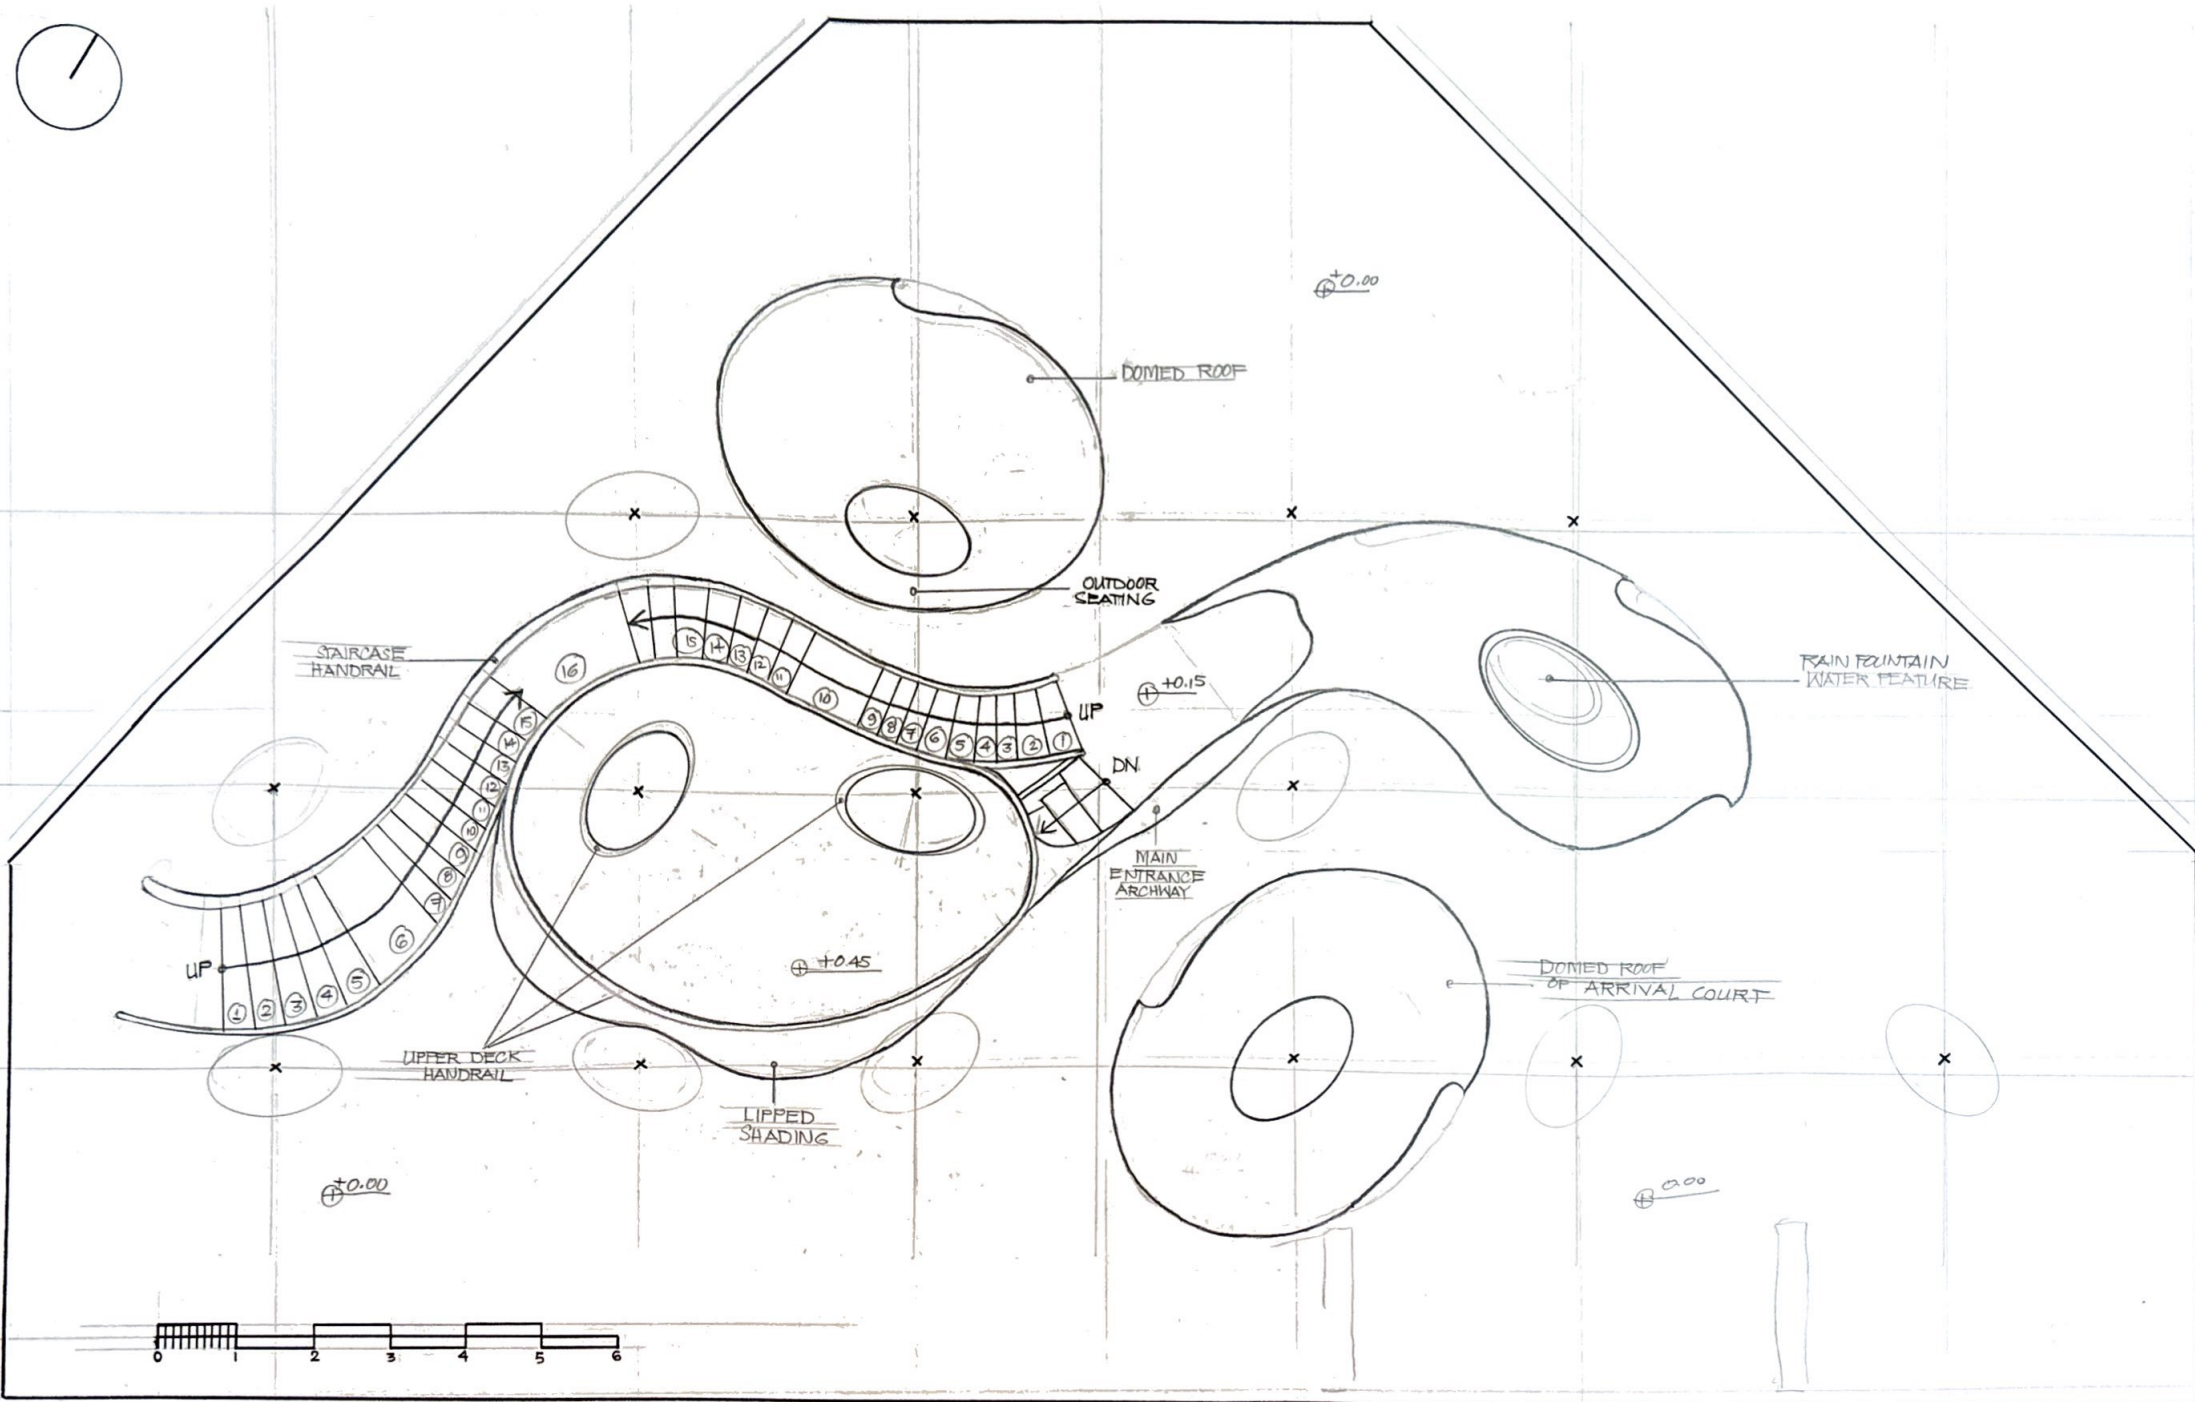

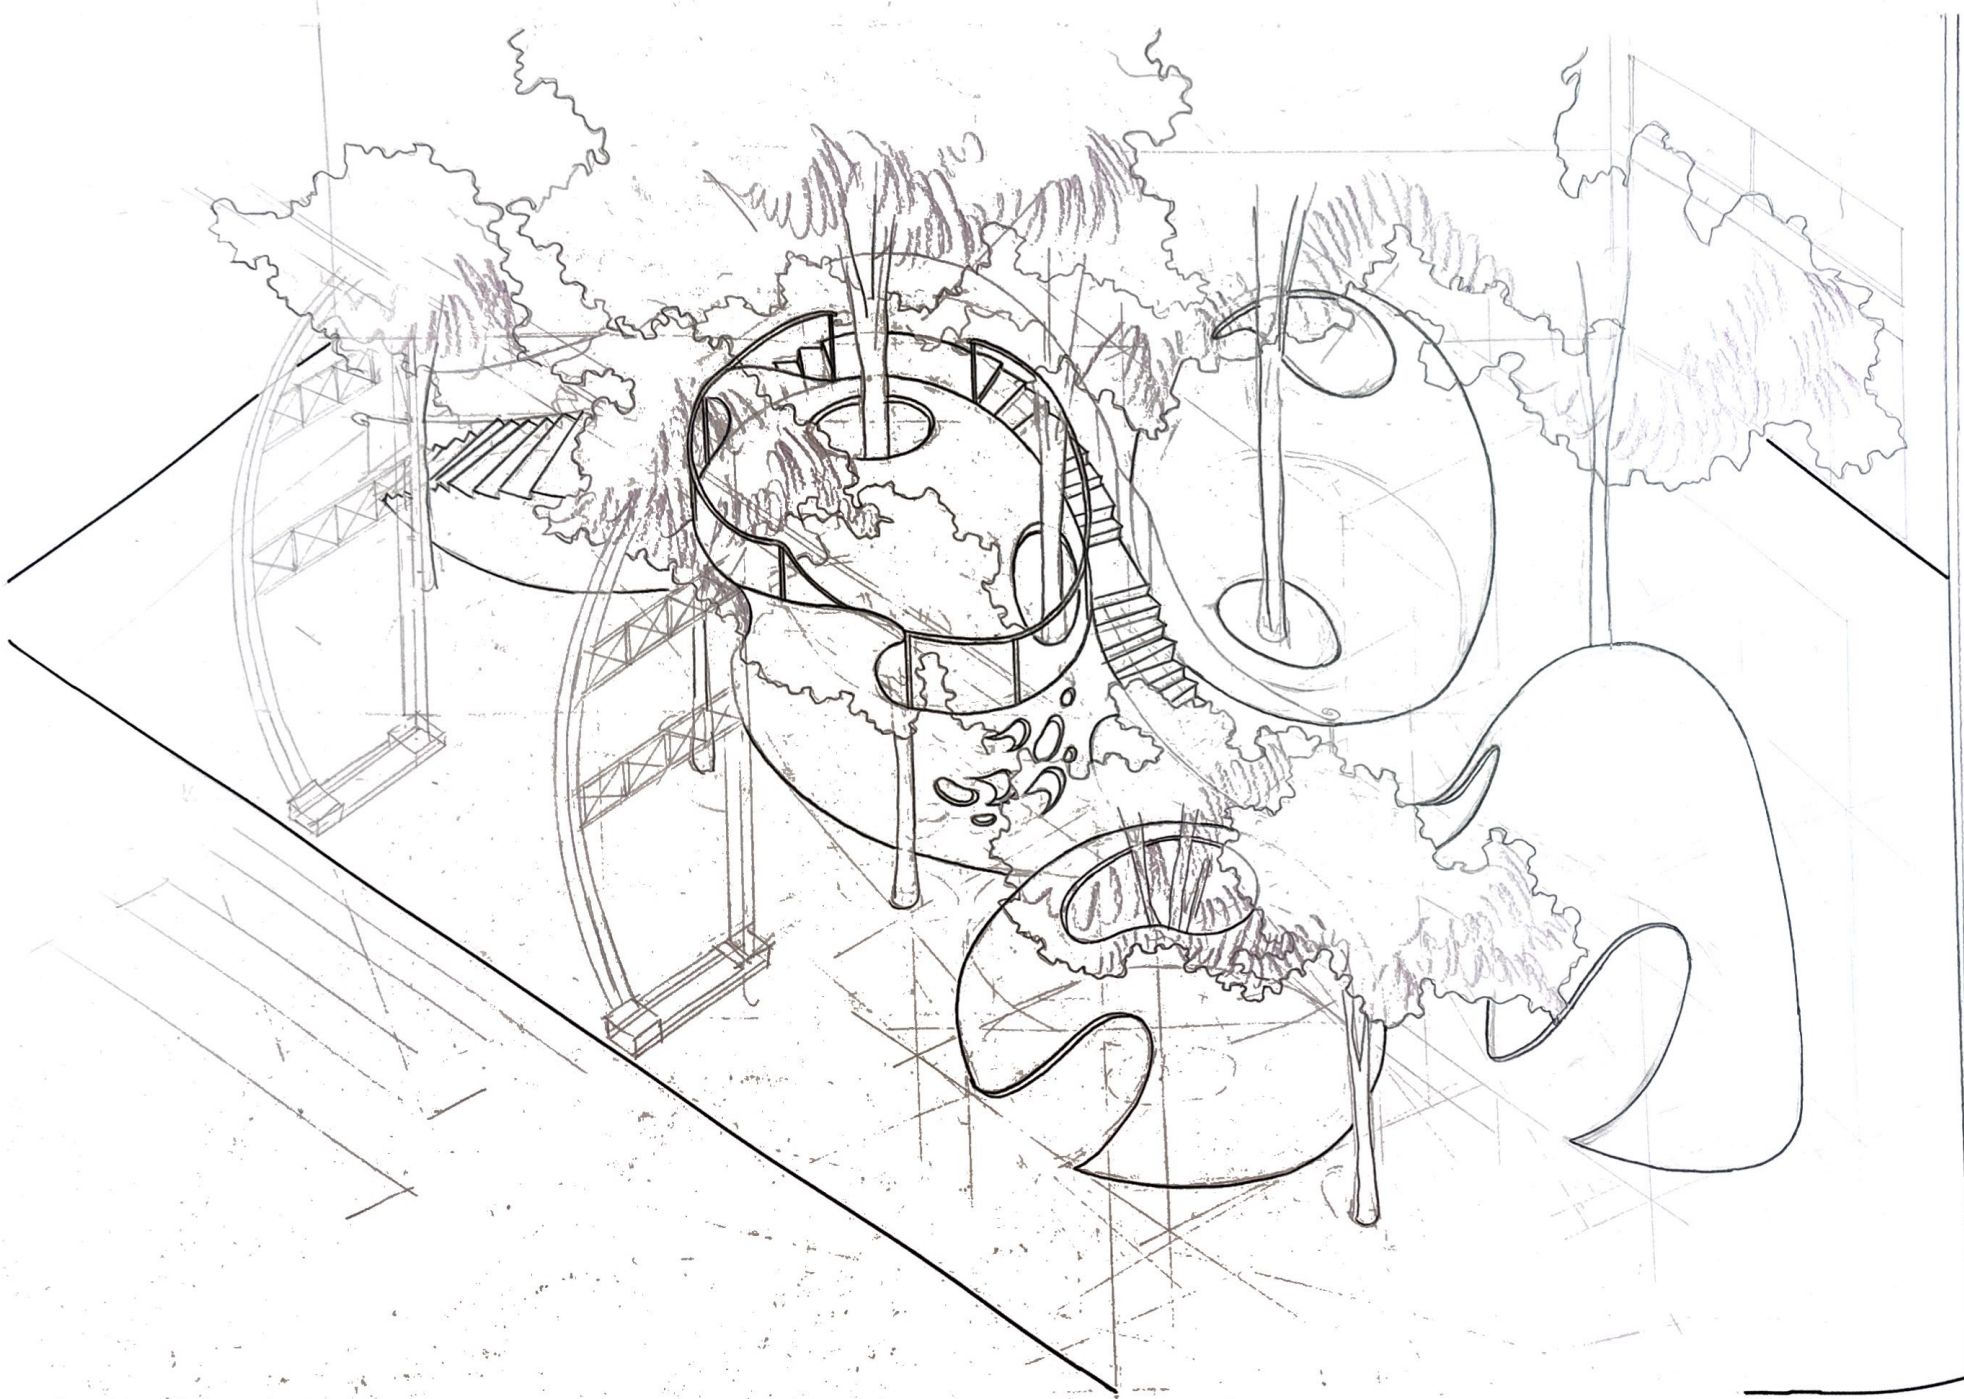

ANNEX

